




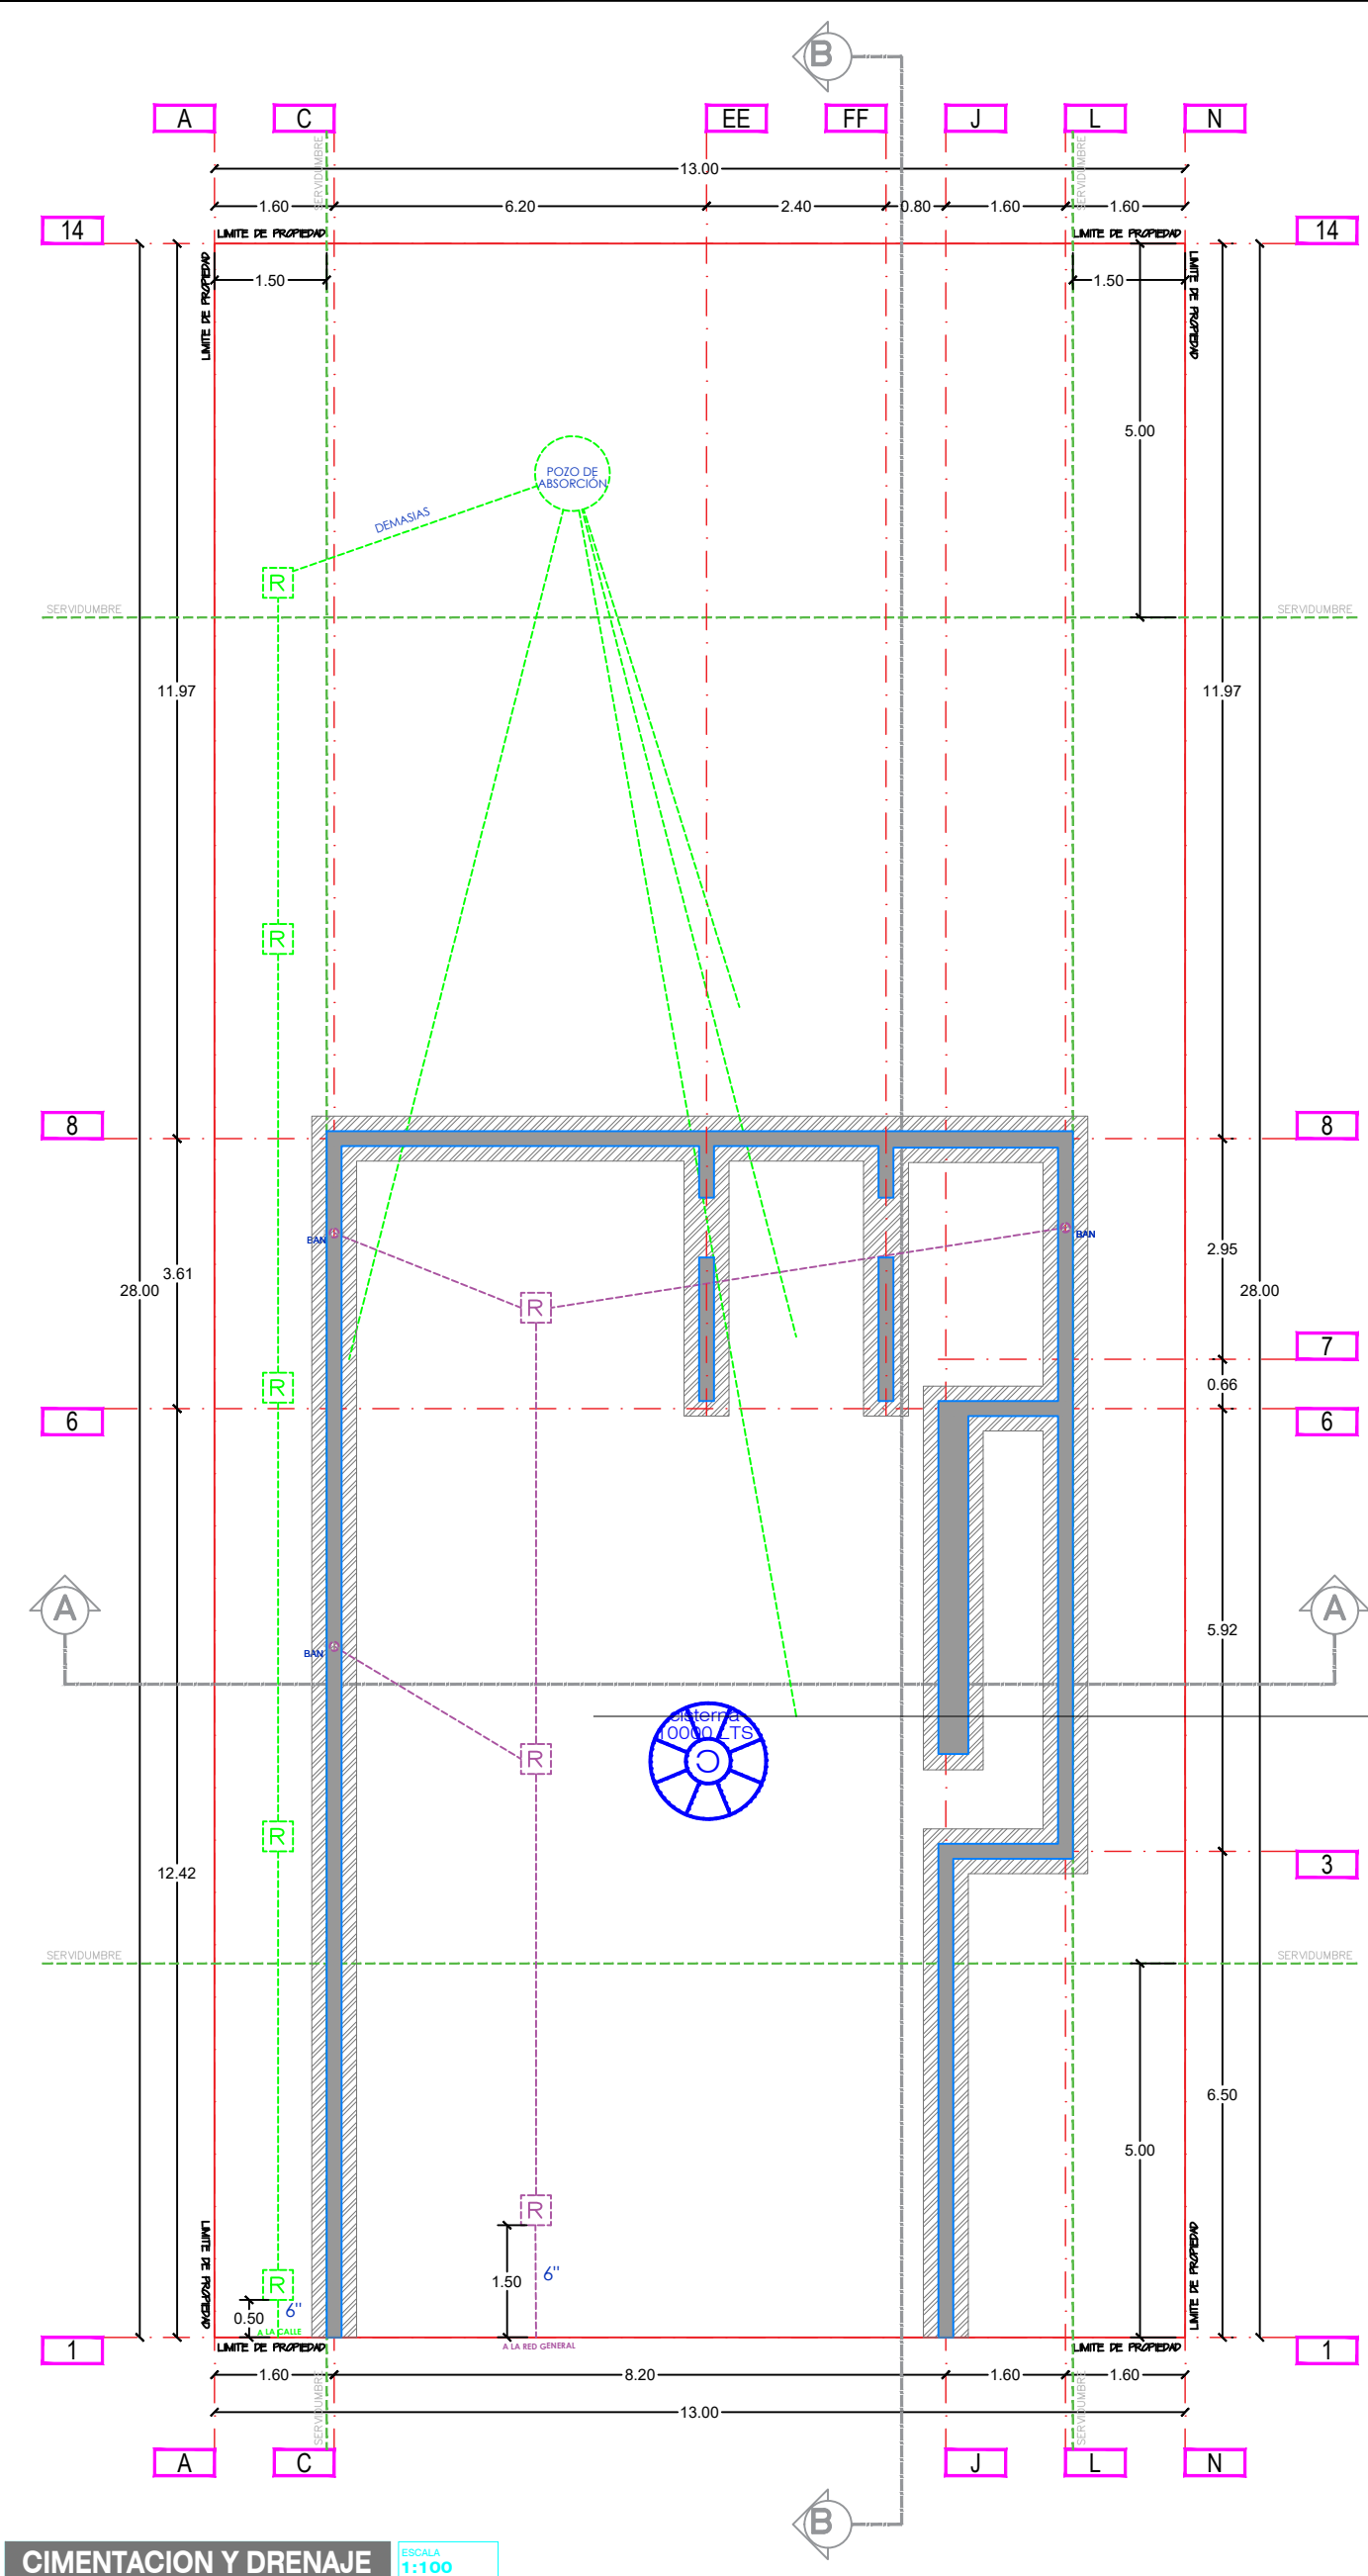


CIMENTACION Y DRENAJE ESCALA 1:100

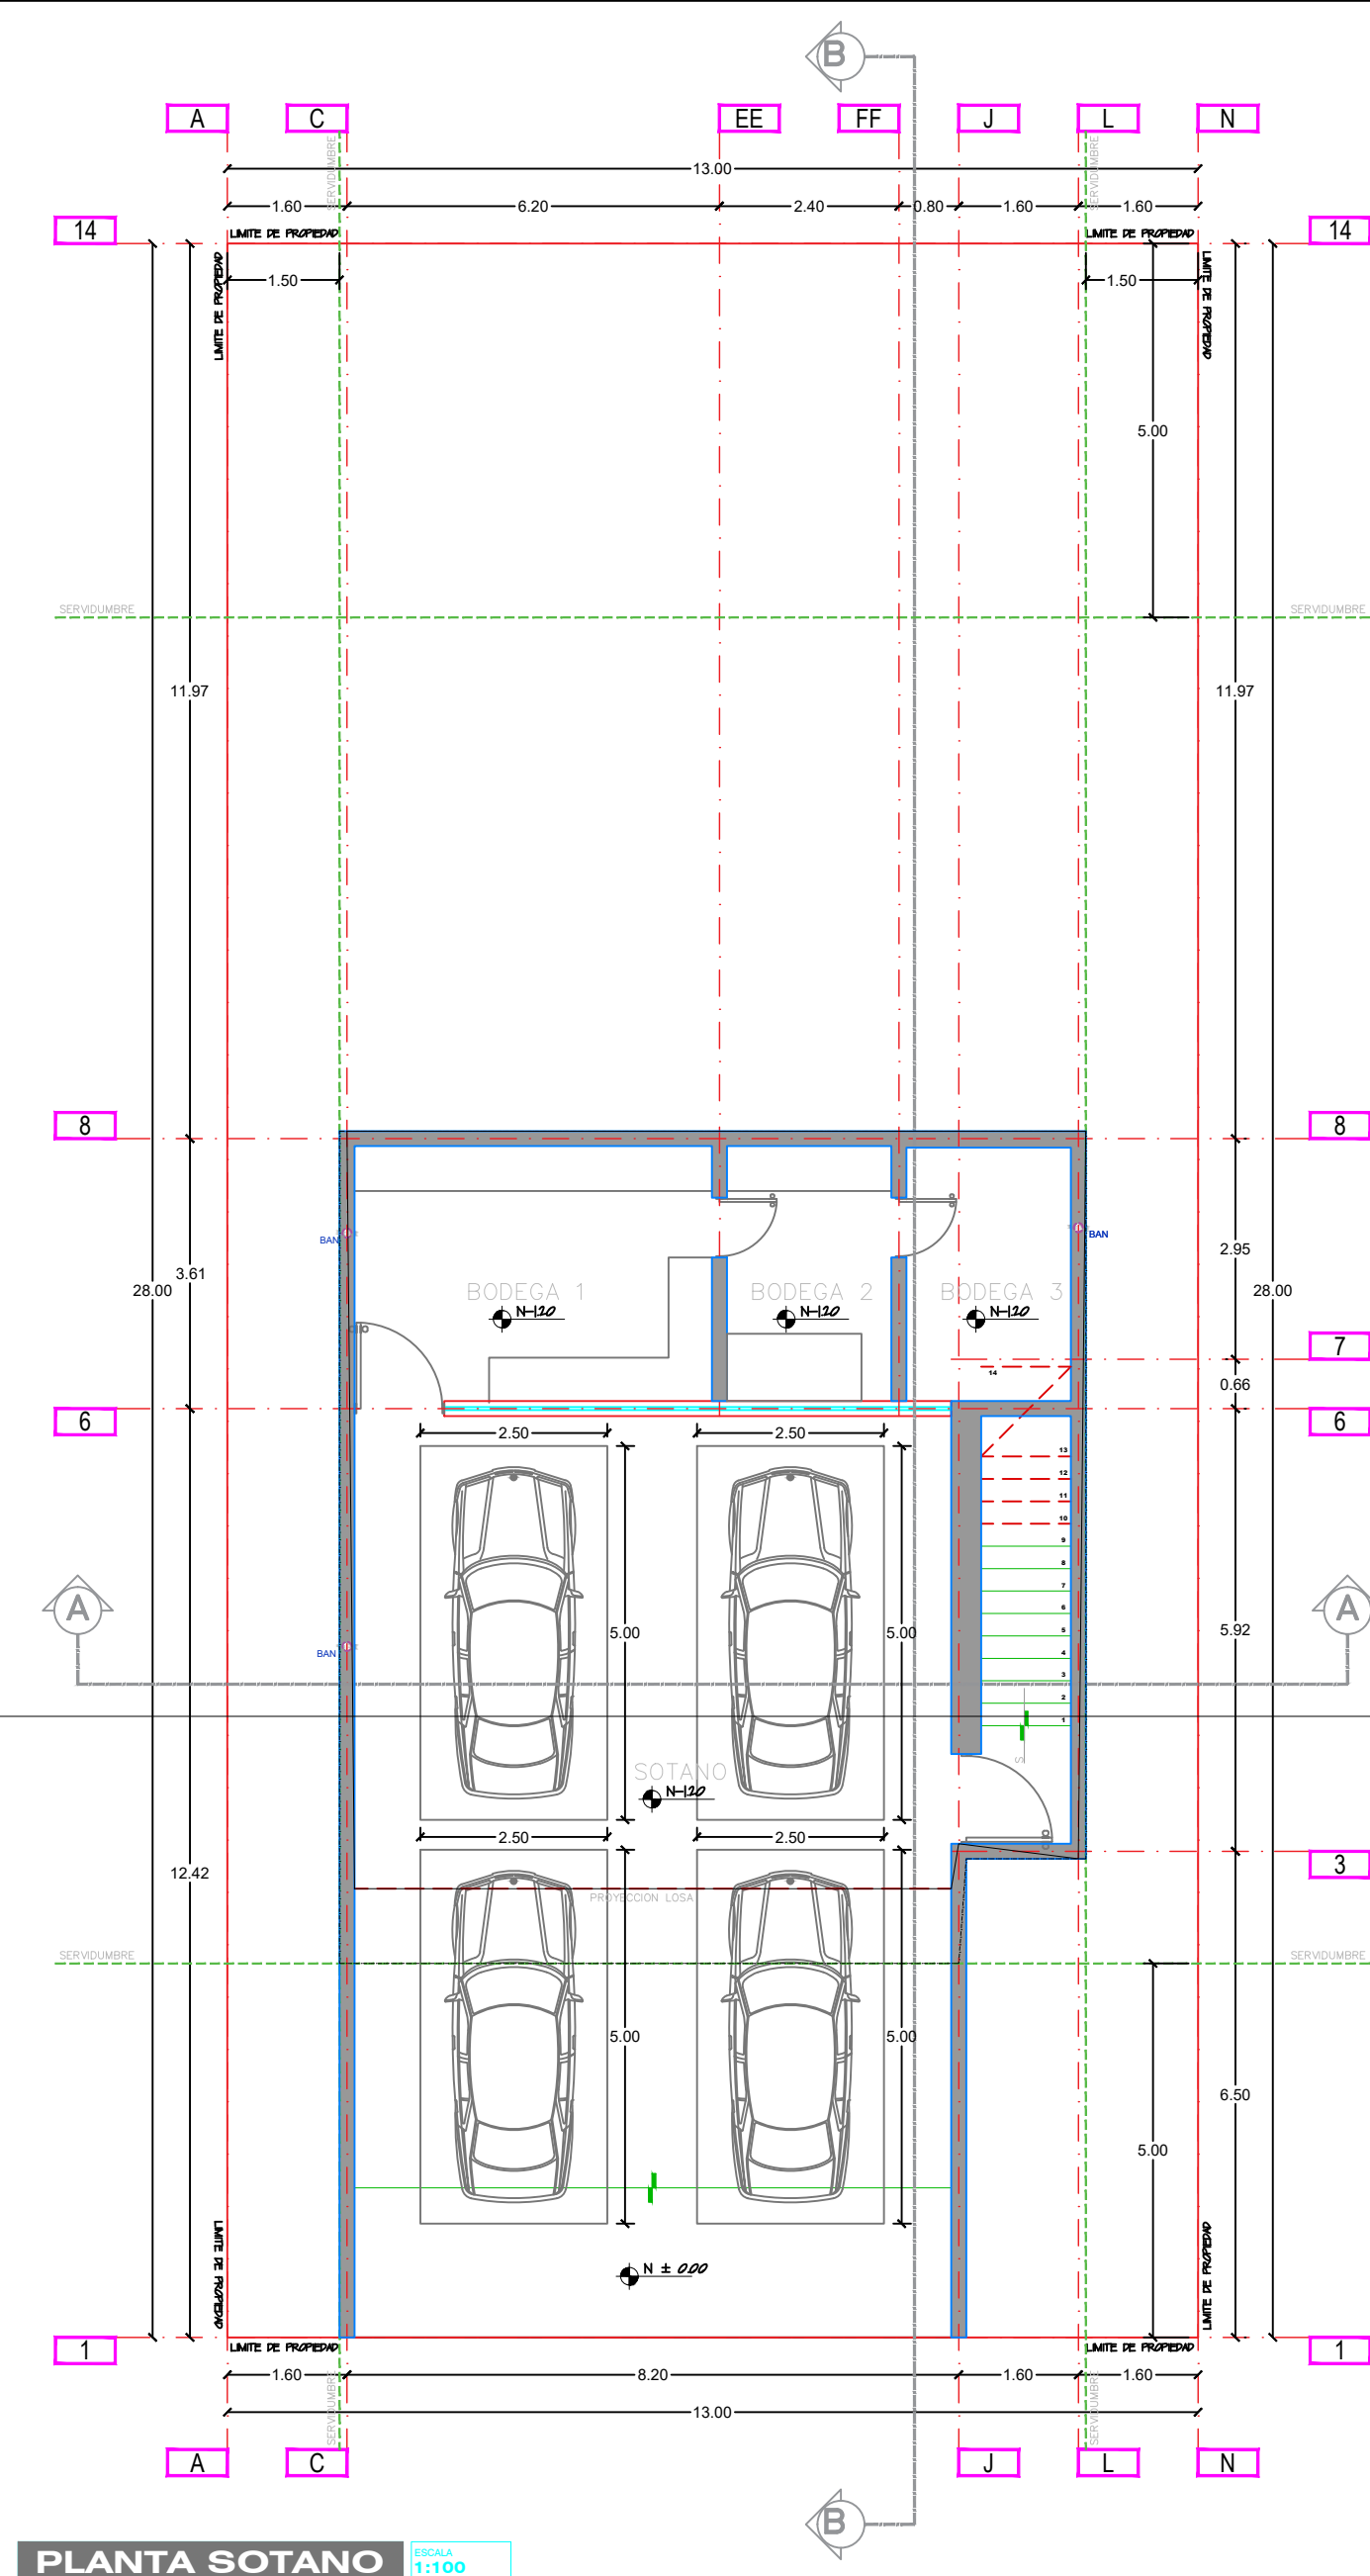


PLANTA SOTANO ESCALA 1:100

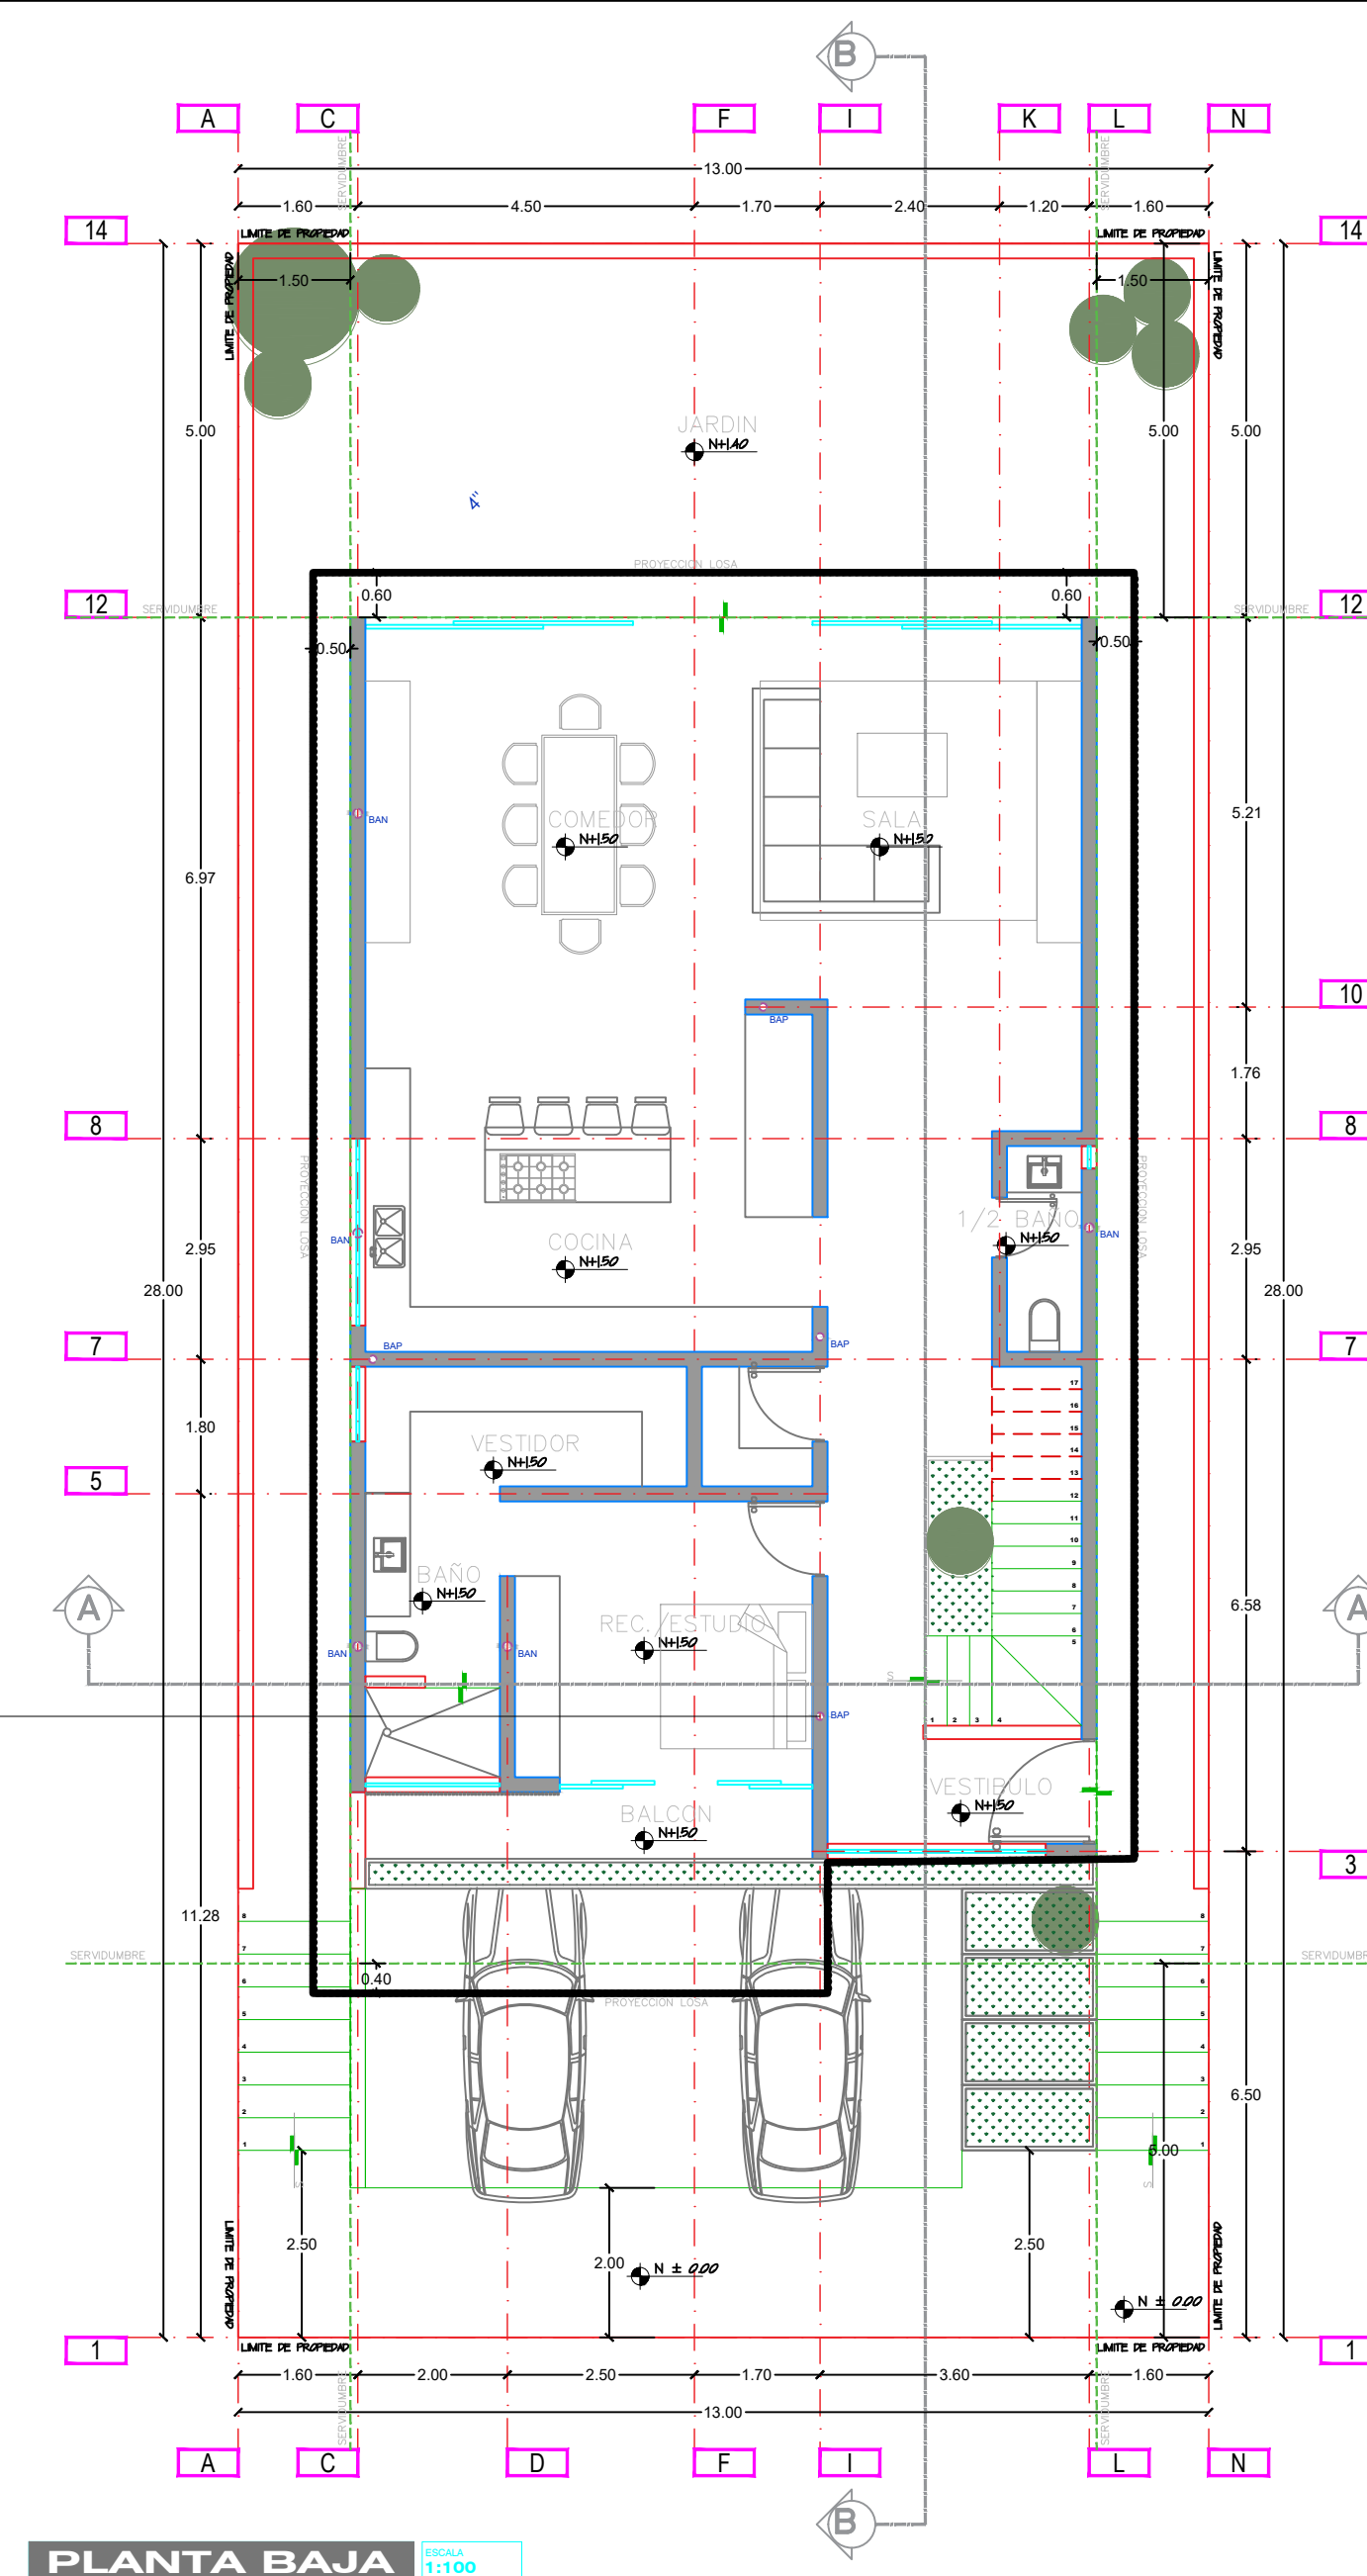


PLANTA BAJA ESCALA 1:100

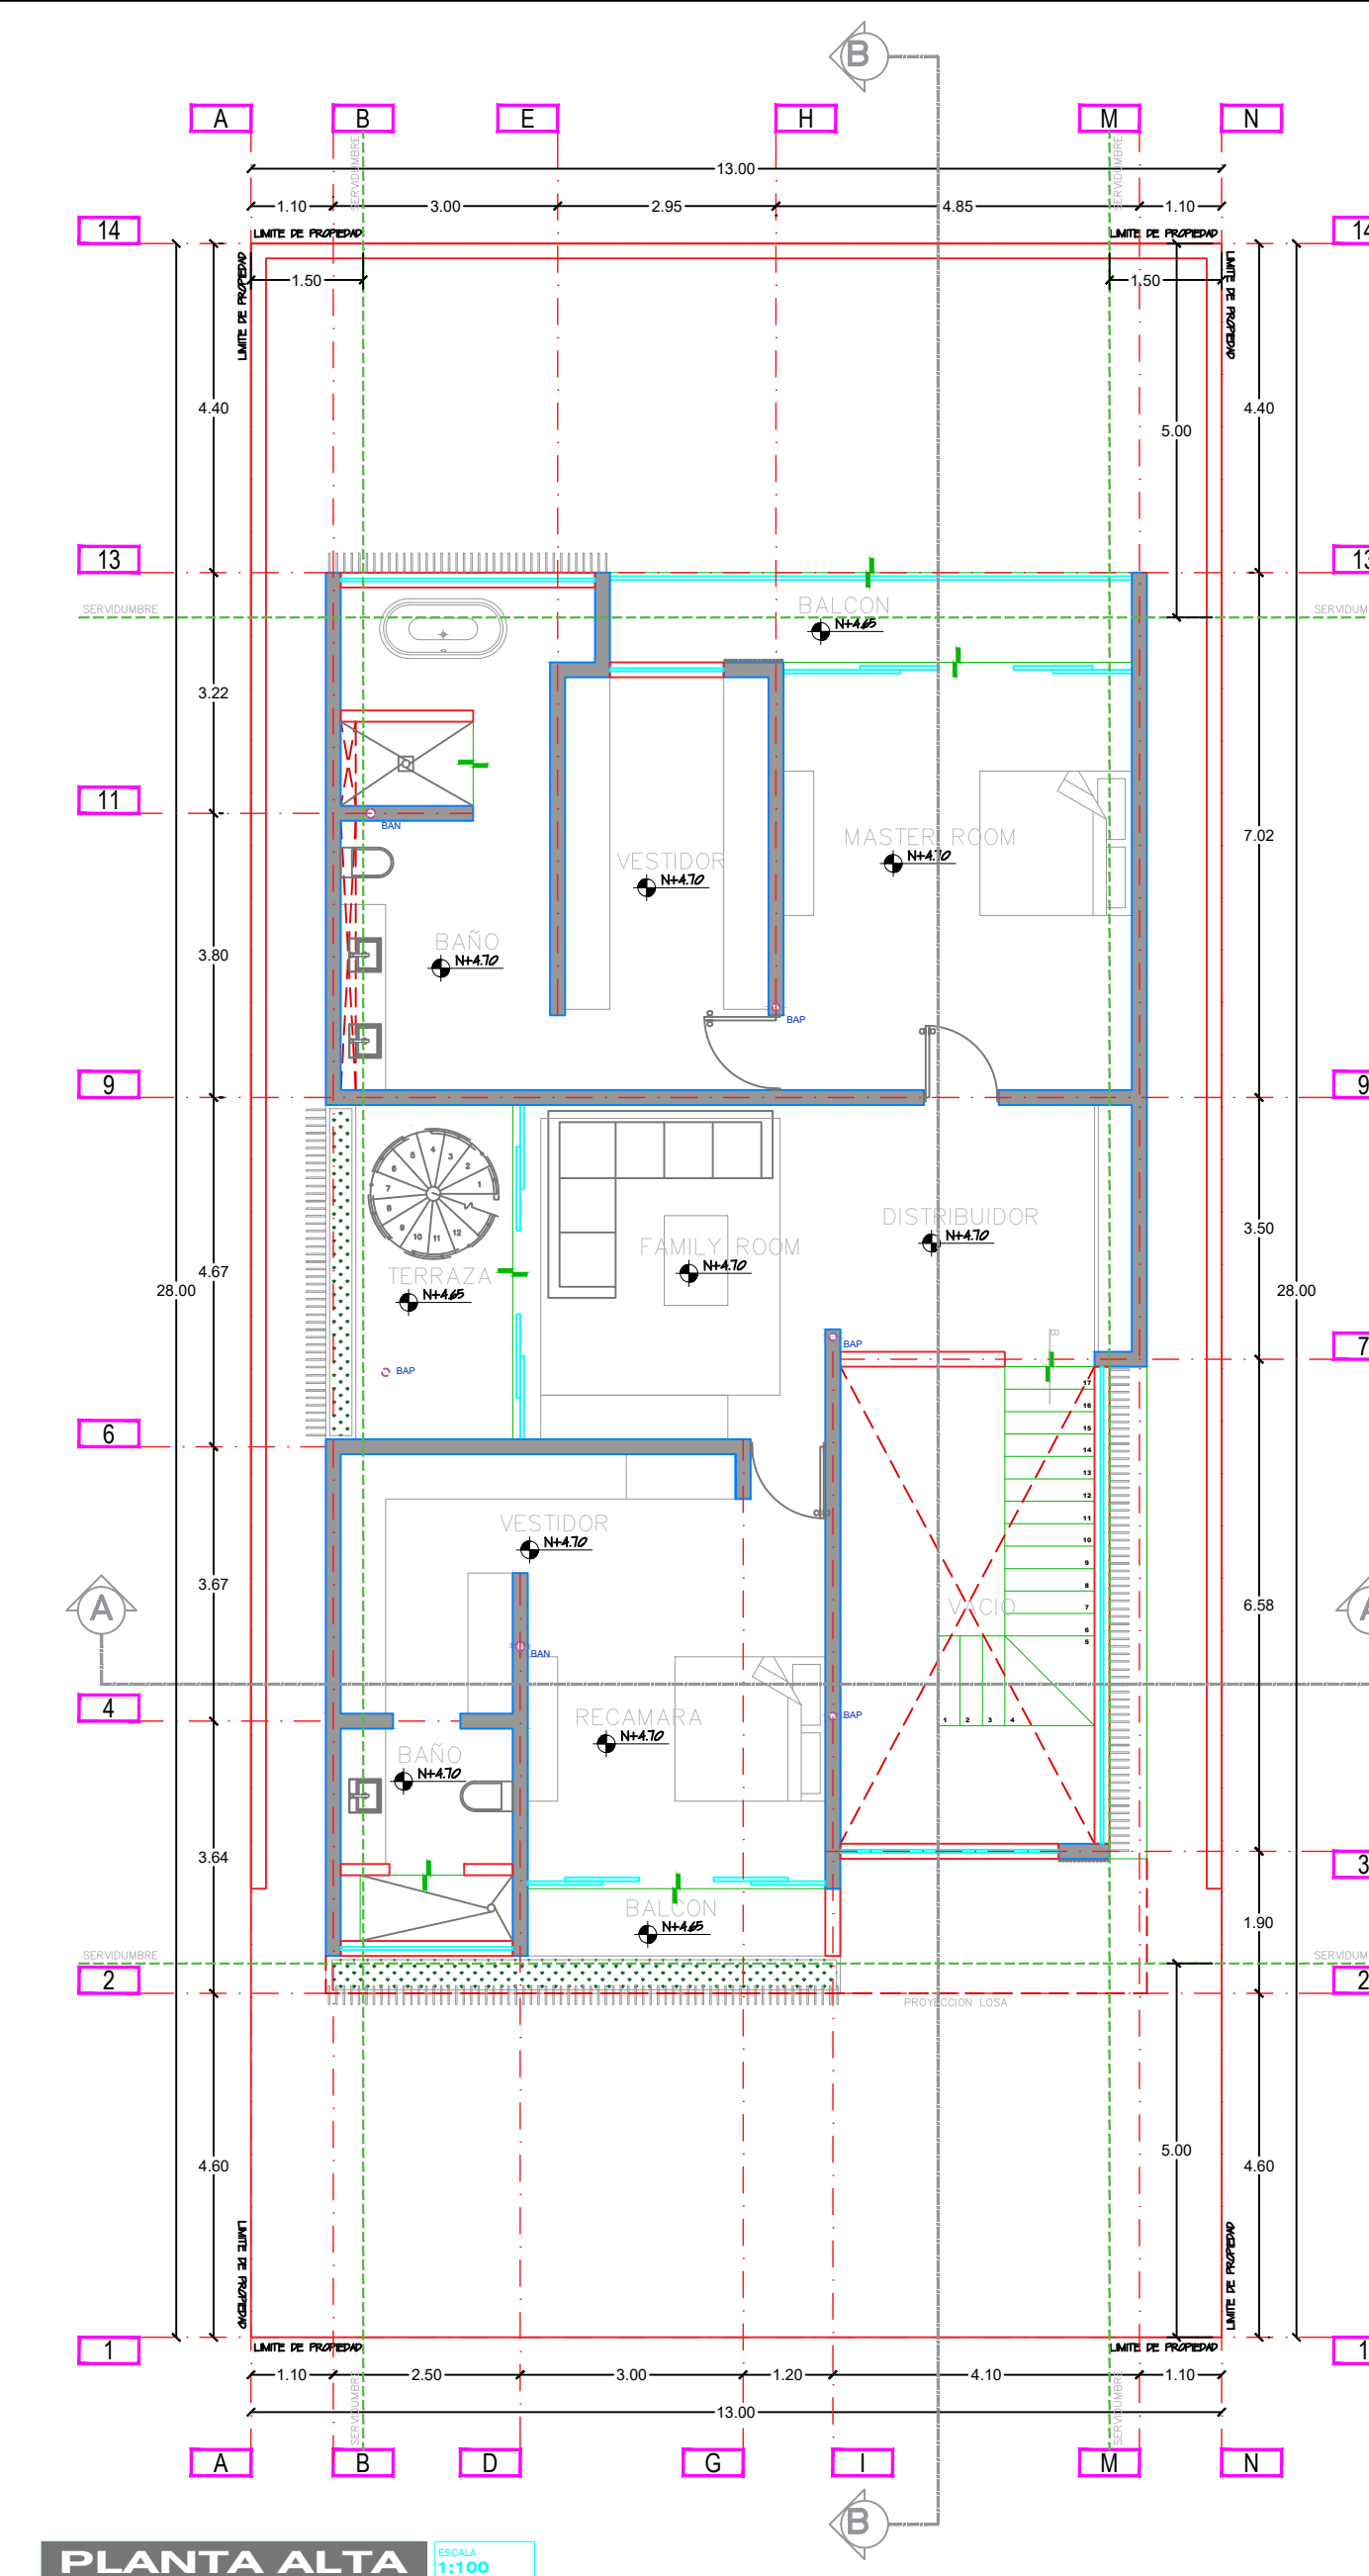


PLANTA ALTA ESCALA 1:100

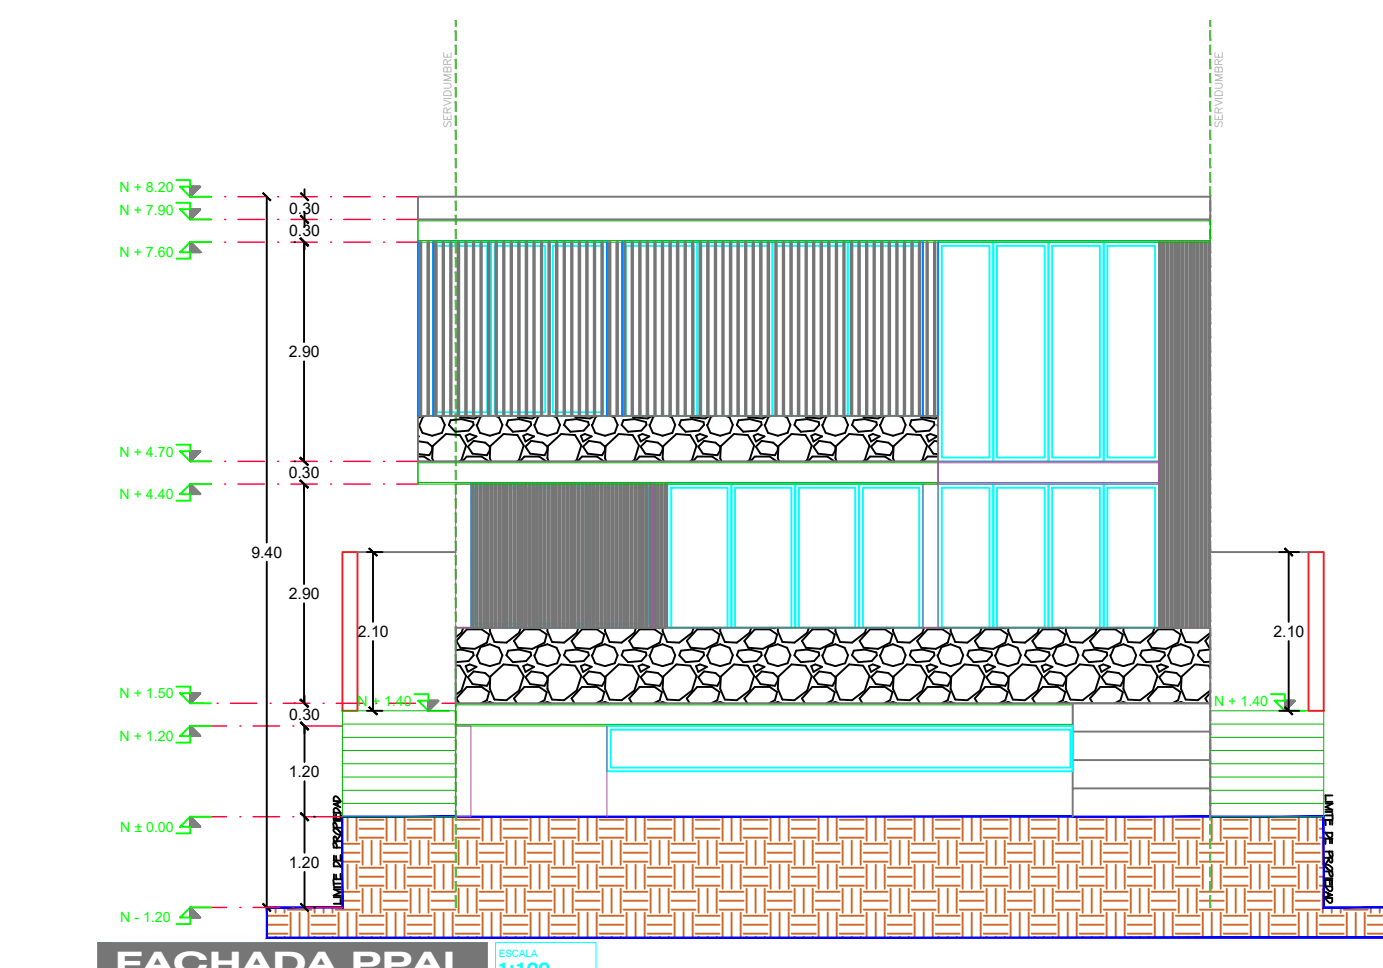

FACHADA PPAL ESCALA 1:100

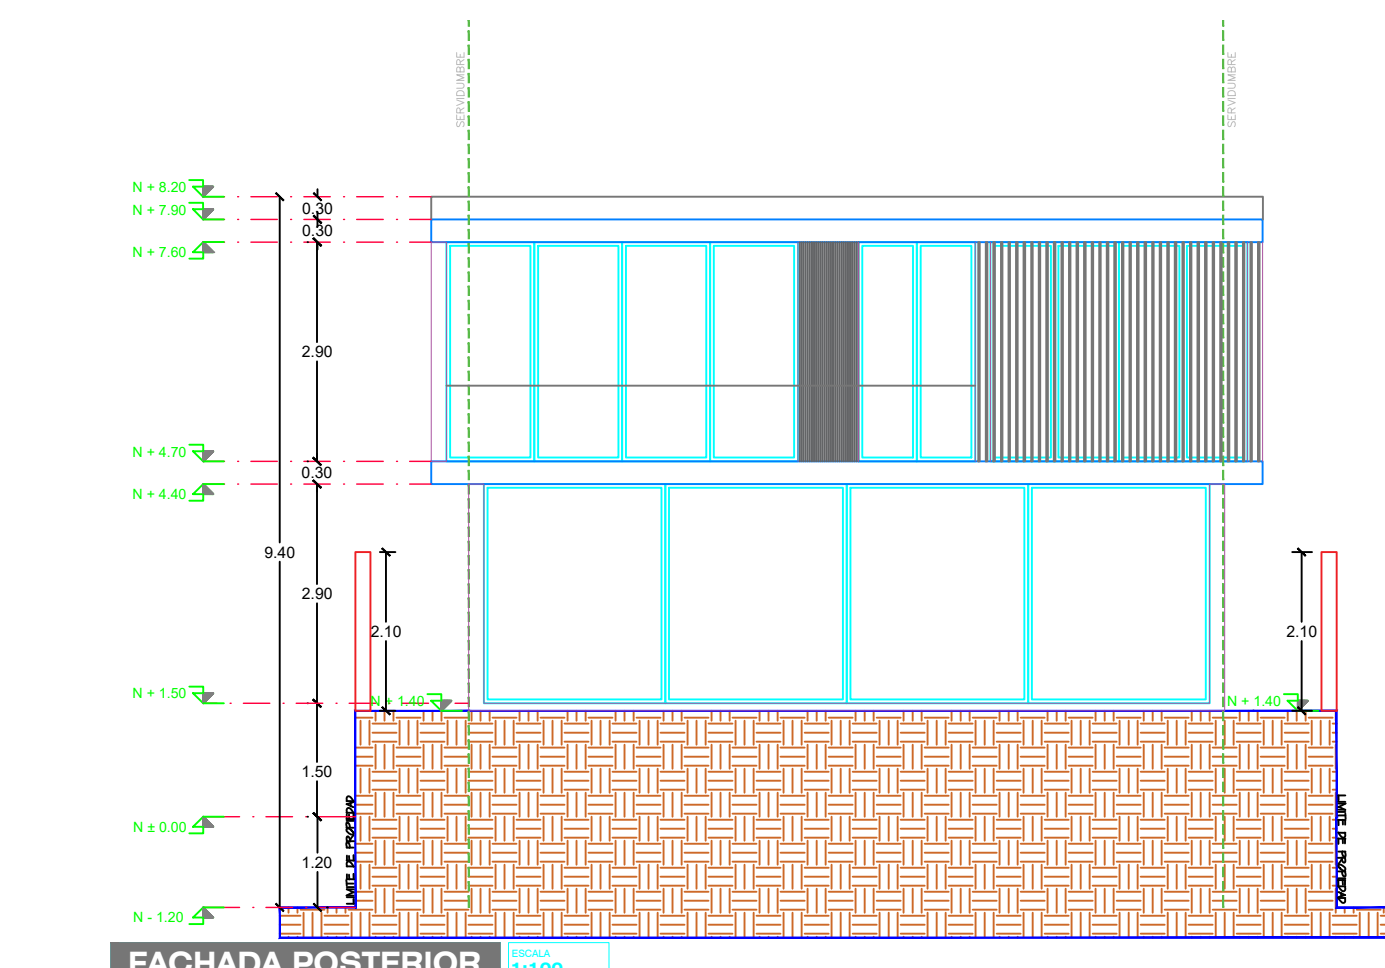

FACHADA POSTERIOR ESCALA 1:100

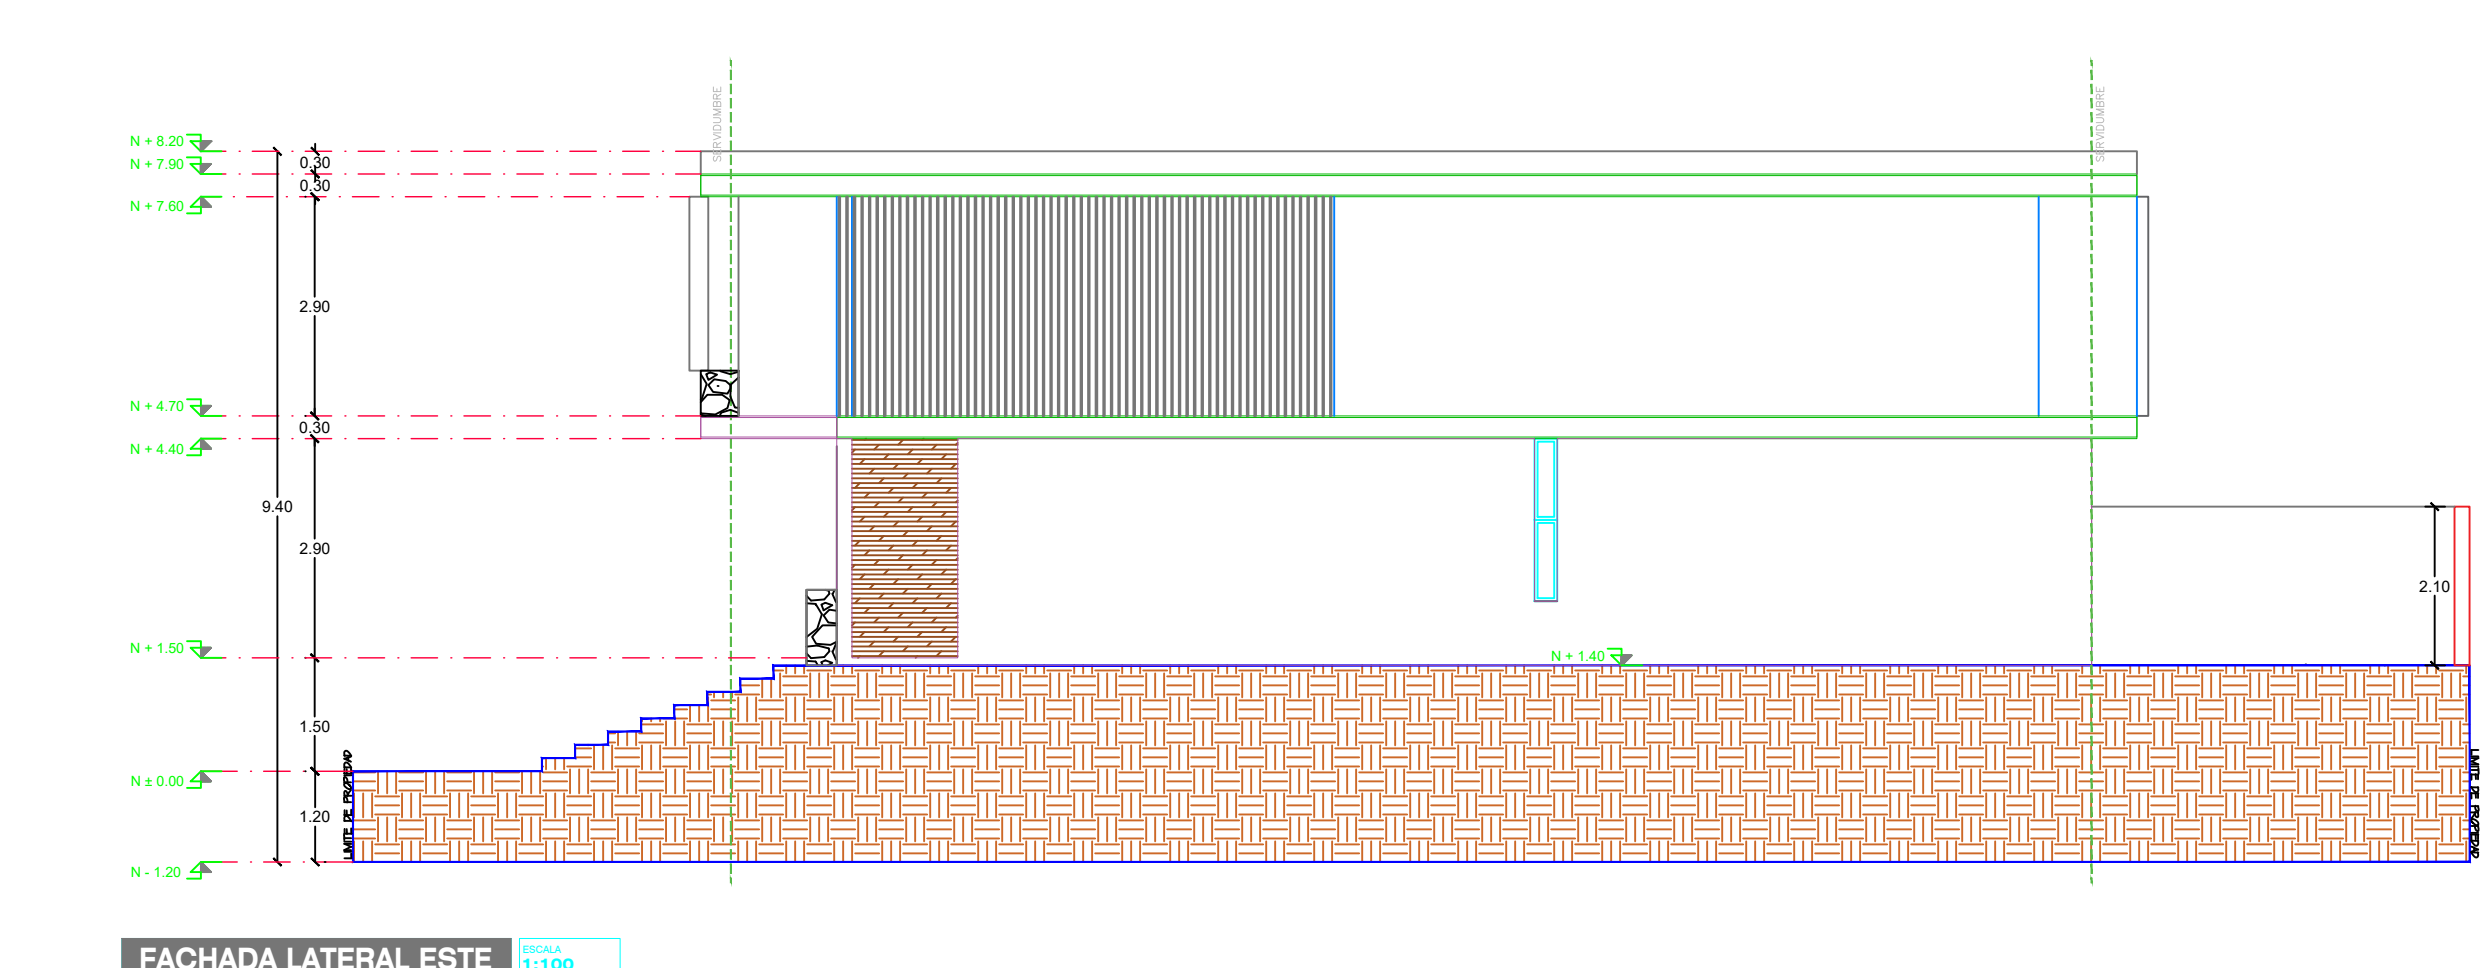

FACHADA LATERAL ESTE ESCALA 1:100

Permisos y  
Licencias de construcción  
Gestión Integral de la Ciudad

UBICACIÓN MACRO:

LOCALIZACIÓN MICRO:

CUADRO DE ÁREAS

|                        | Unidad | Propuesto |
|------------------------|--------|-----------|
| SUPERFICIE DEL TERRENO | m2     | 364.00 m2 |
| SOTANO                 | m2     | 150.73 m2 |
| PLANTA BAJA            | m2     | 186.35 m2 |
| PLANTA ALTA            | m2     | 198.34 m2 |
| AZOTEA                 | m2     | —         |
| TOTAL                  | m2     | 535.42 m2 |
| BARDEO                 | ml     | 57.00 ml  |
| CISTERNA               | m3     | 10.00 m3  |

NOTA: CUALQUIER ELEMENTO CONSTRUCTIVO NO SEÑALADO DEBERÁ ANOTARSE EN ESTE RECUADRO.

COEFICIENTES

|            | C.O.S.      | C.U.S.      |
|------------|-------------|-------------|
| PERMITIDO  | 0.6 218 m2  | 1.2 436 m2  |
| PROYECTADO | 0.42 187 m2 | 1.06 385 m2 |

SIMBOLOGÍA

DATOS DEL PREDIO

CALLE: General Río San Francisco

NÚMERO: CONDOMINIO: ARAUCA II

LOTE 182 MANZANA UP

COLONIA: ARAUCA II

PROPIETARIO(S)

DIETER BÜCHNER

FIRMA

DIRECTOR RESPONSABLE EN PROYECTO Y OBRA

RICARDO ORTIZ FLORES

DRZ- 0424/2025

FIRMA

DIBUJO: SYD CONSTRUCTORES

TÍTULO

CASA ARAUCA






CONTENIDO

PLANTAS ARQUITECTONICAS,  
FACHADAS

ESCALA 1:100

FECHA MARZO 2026


NÚMERO DE LÁMINA 1/2

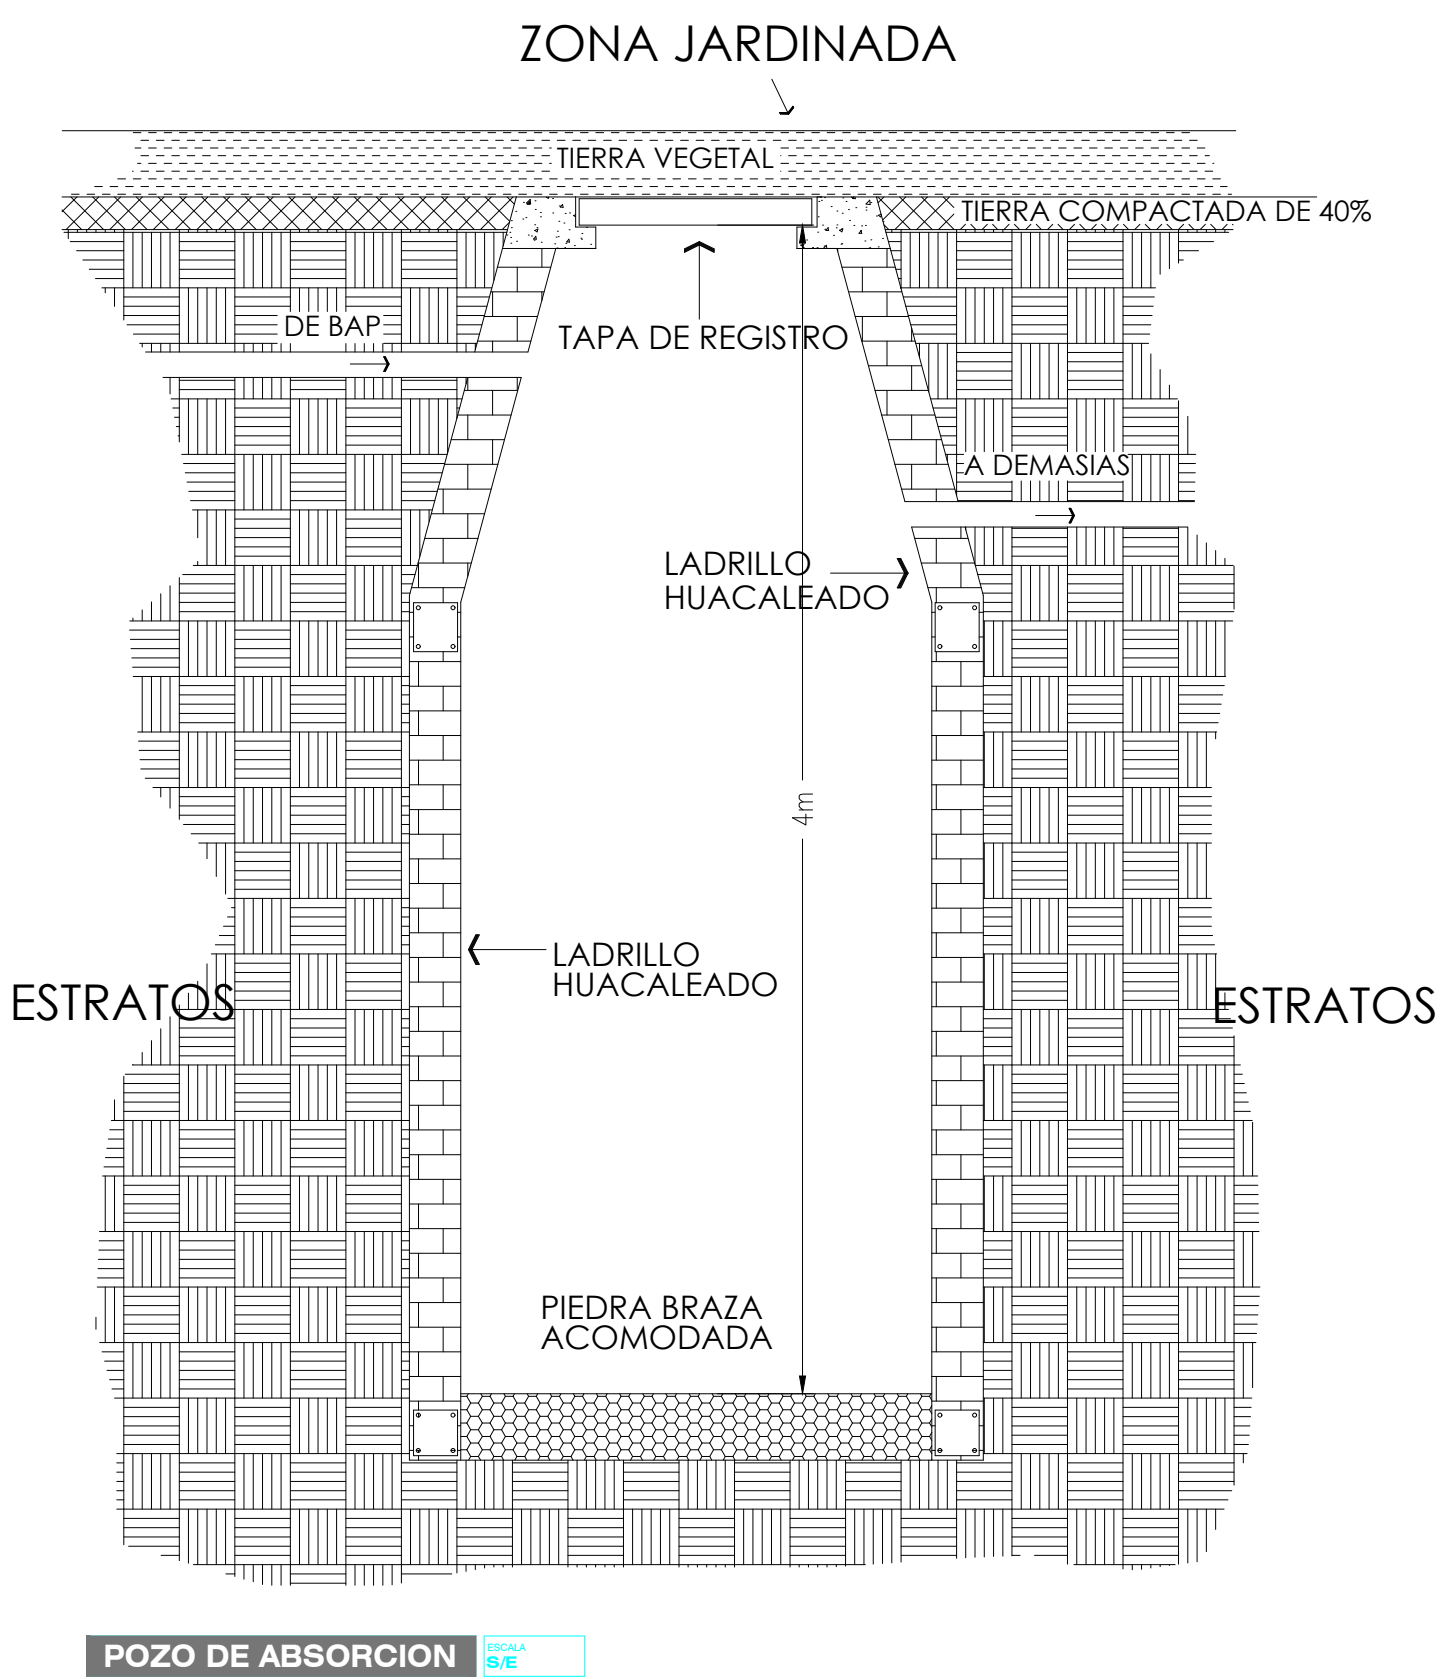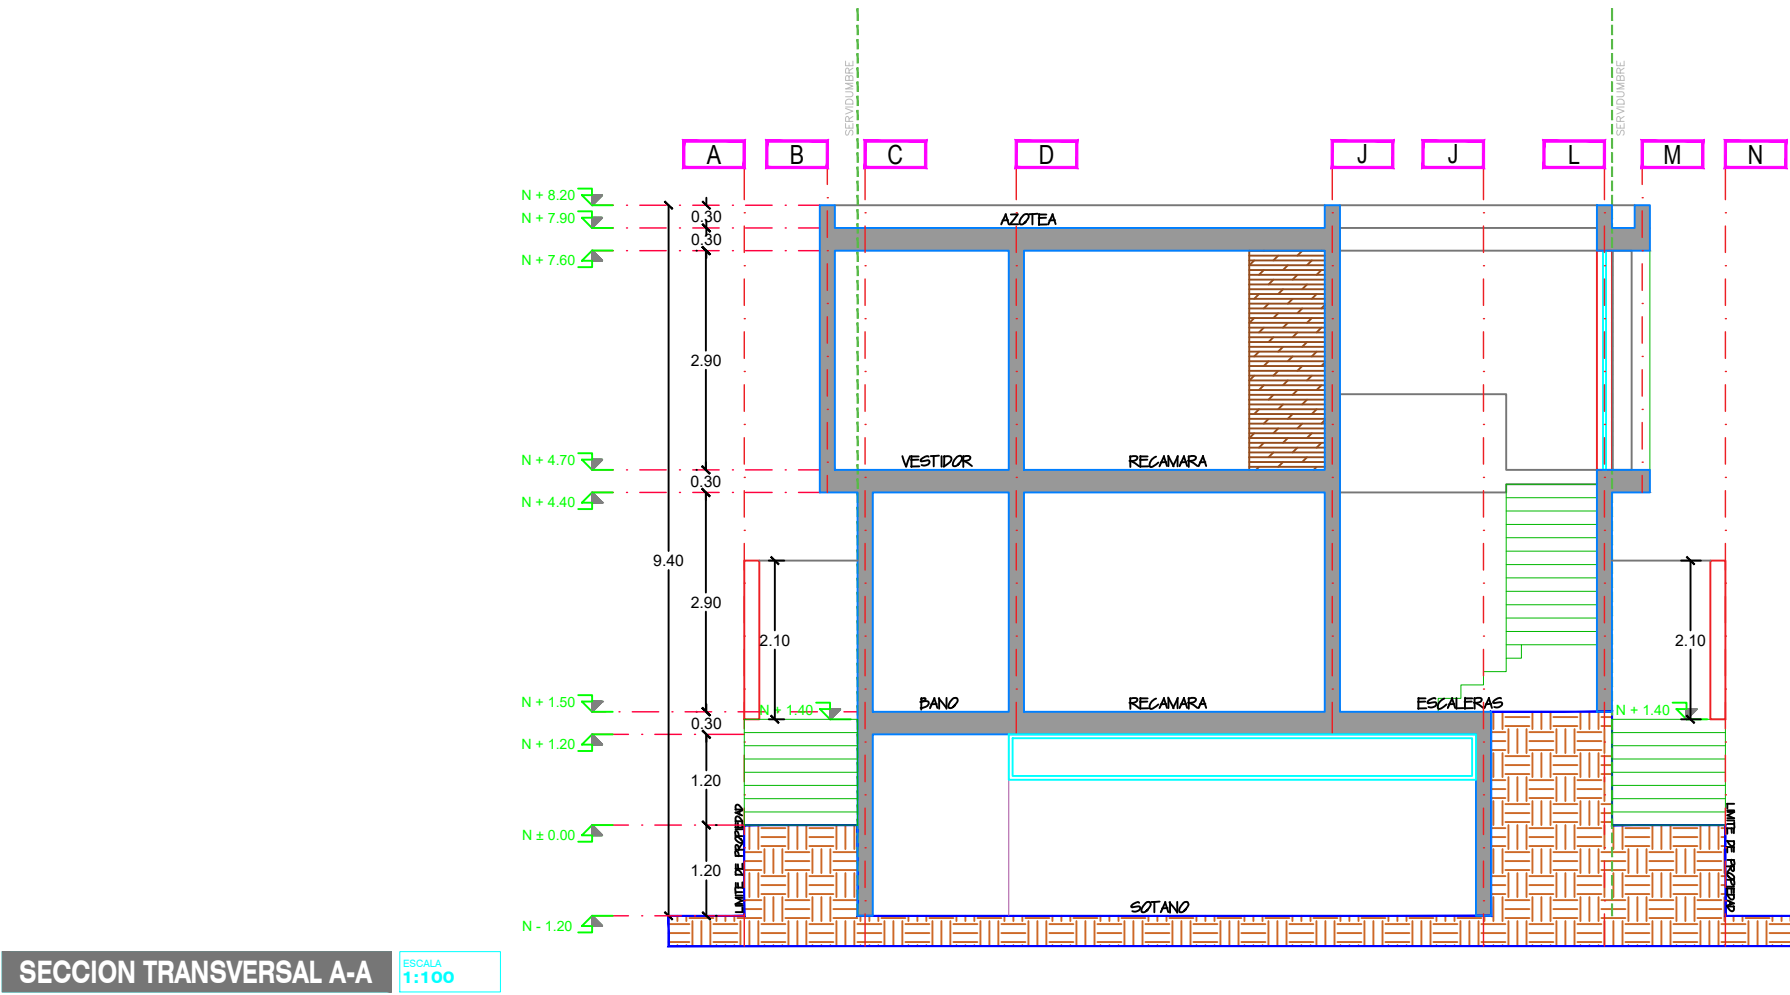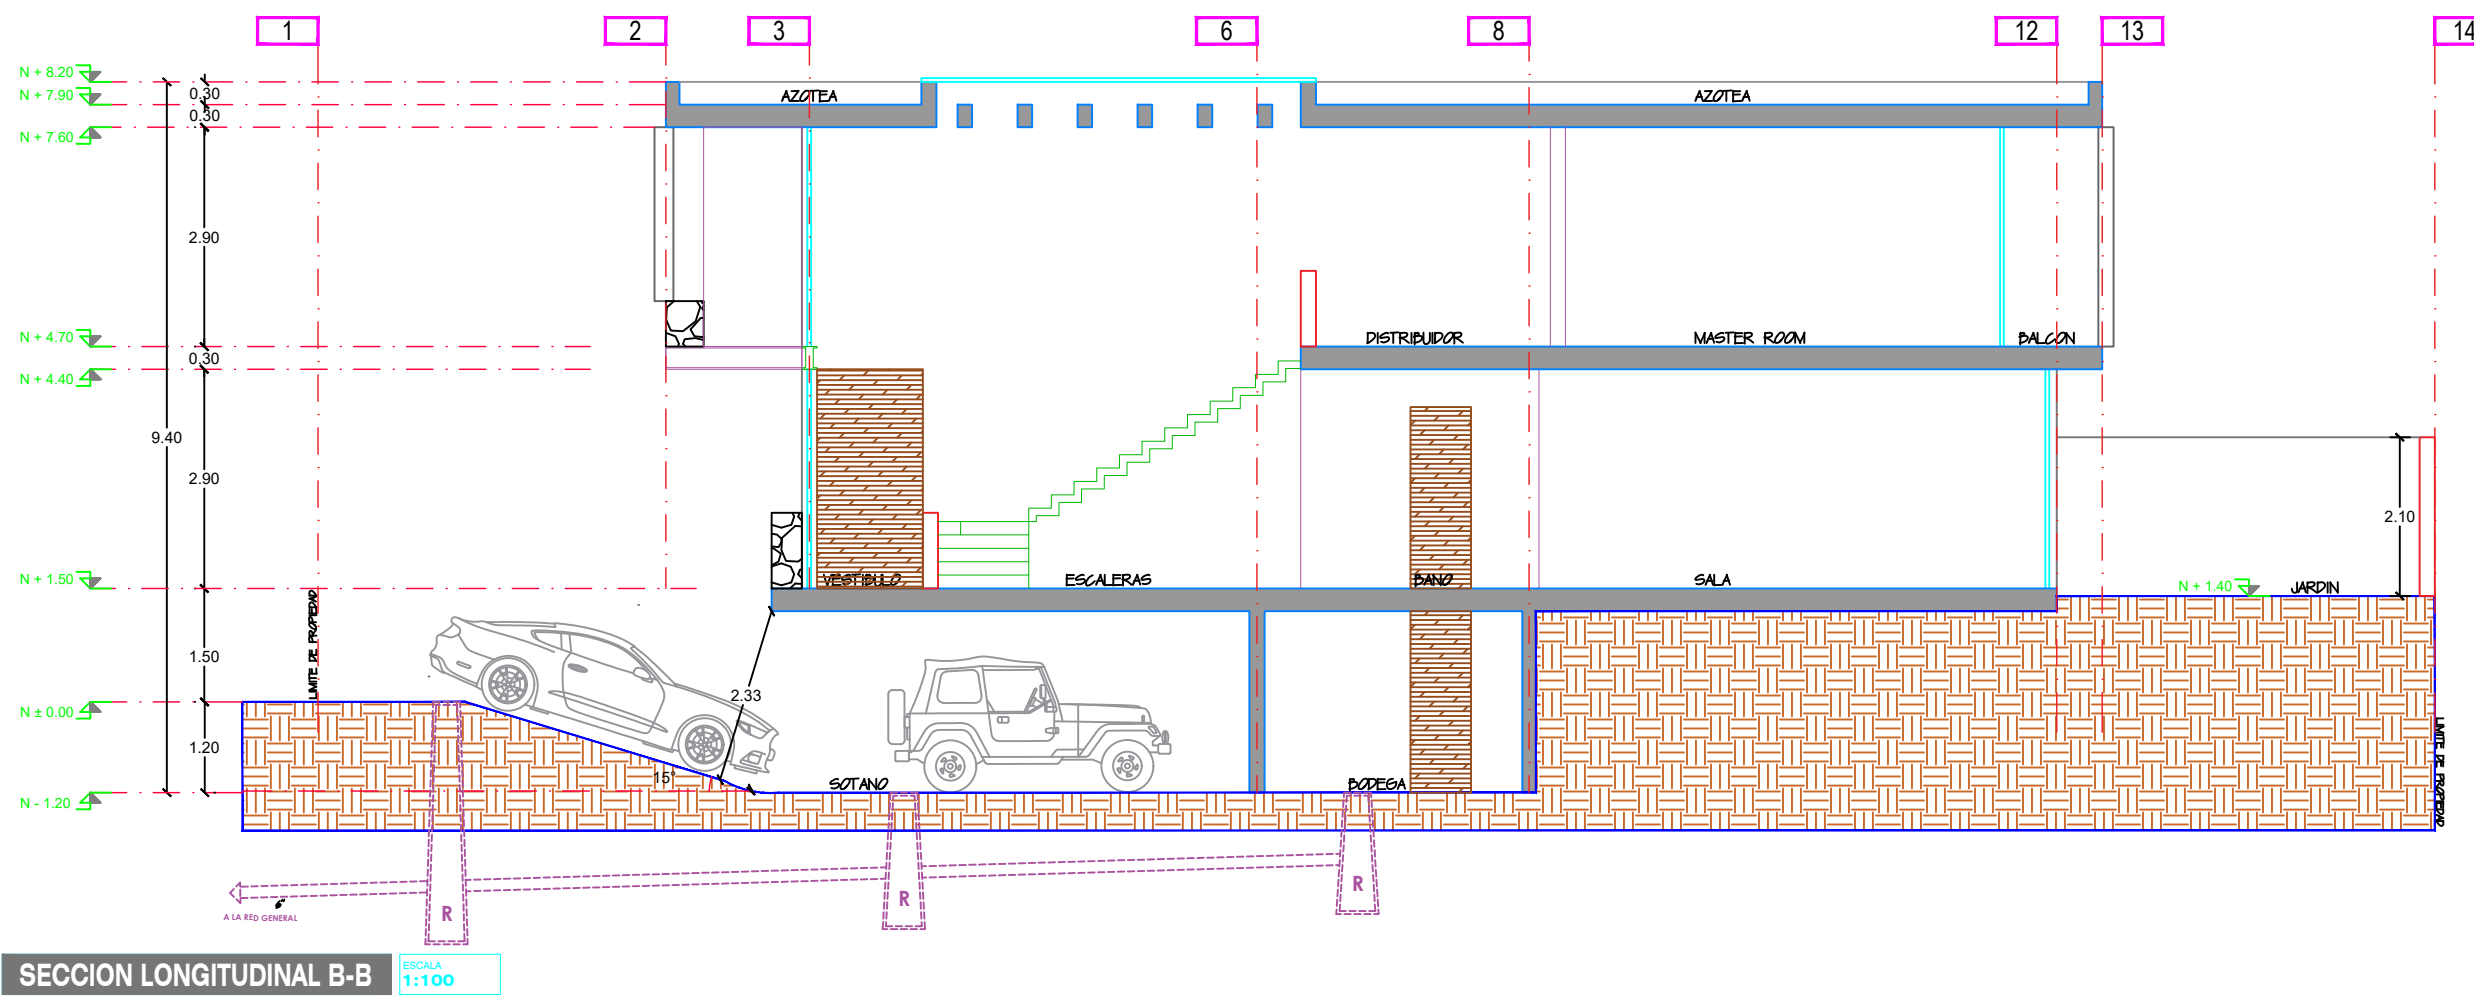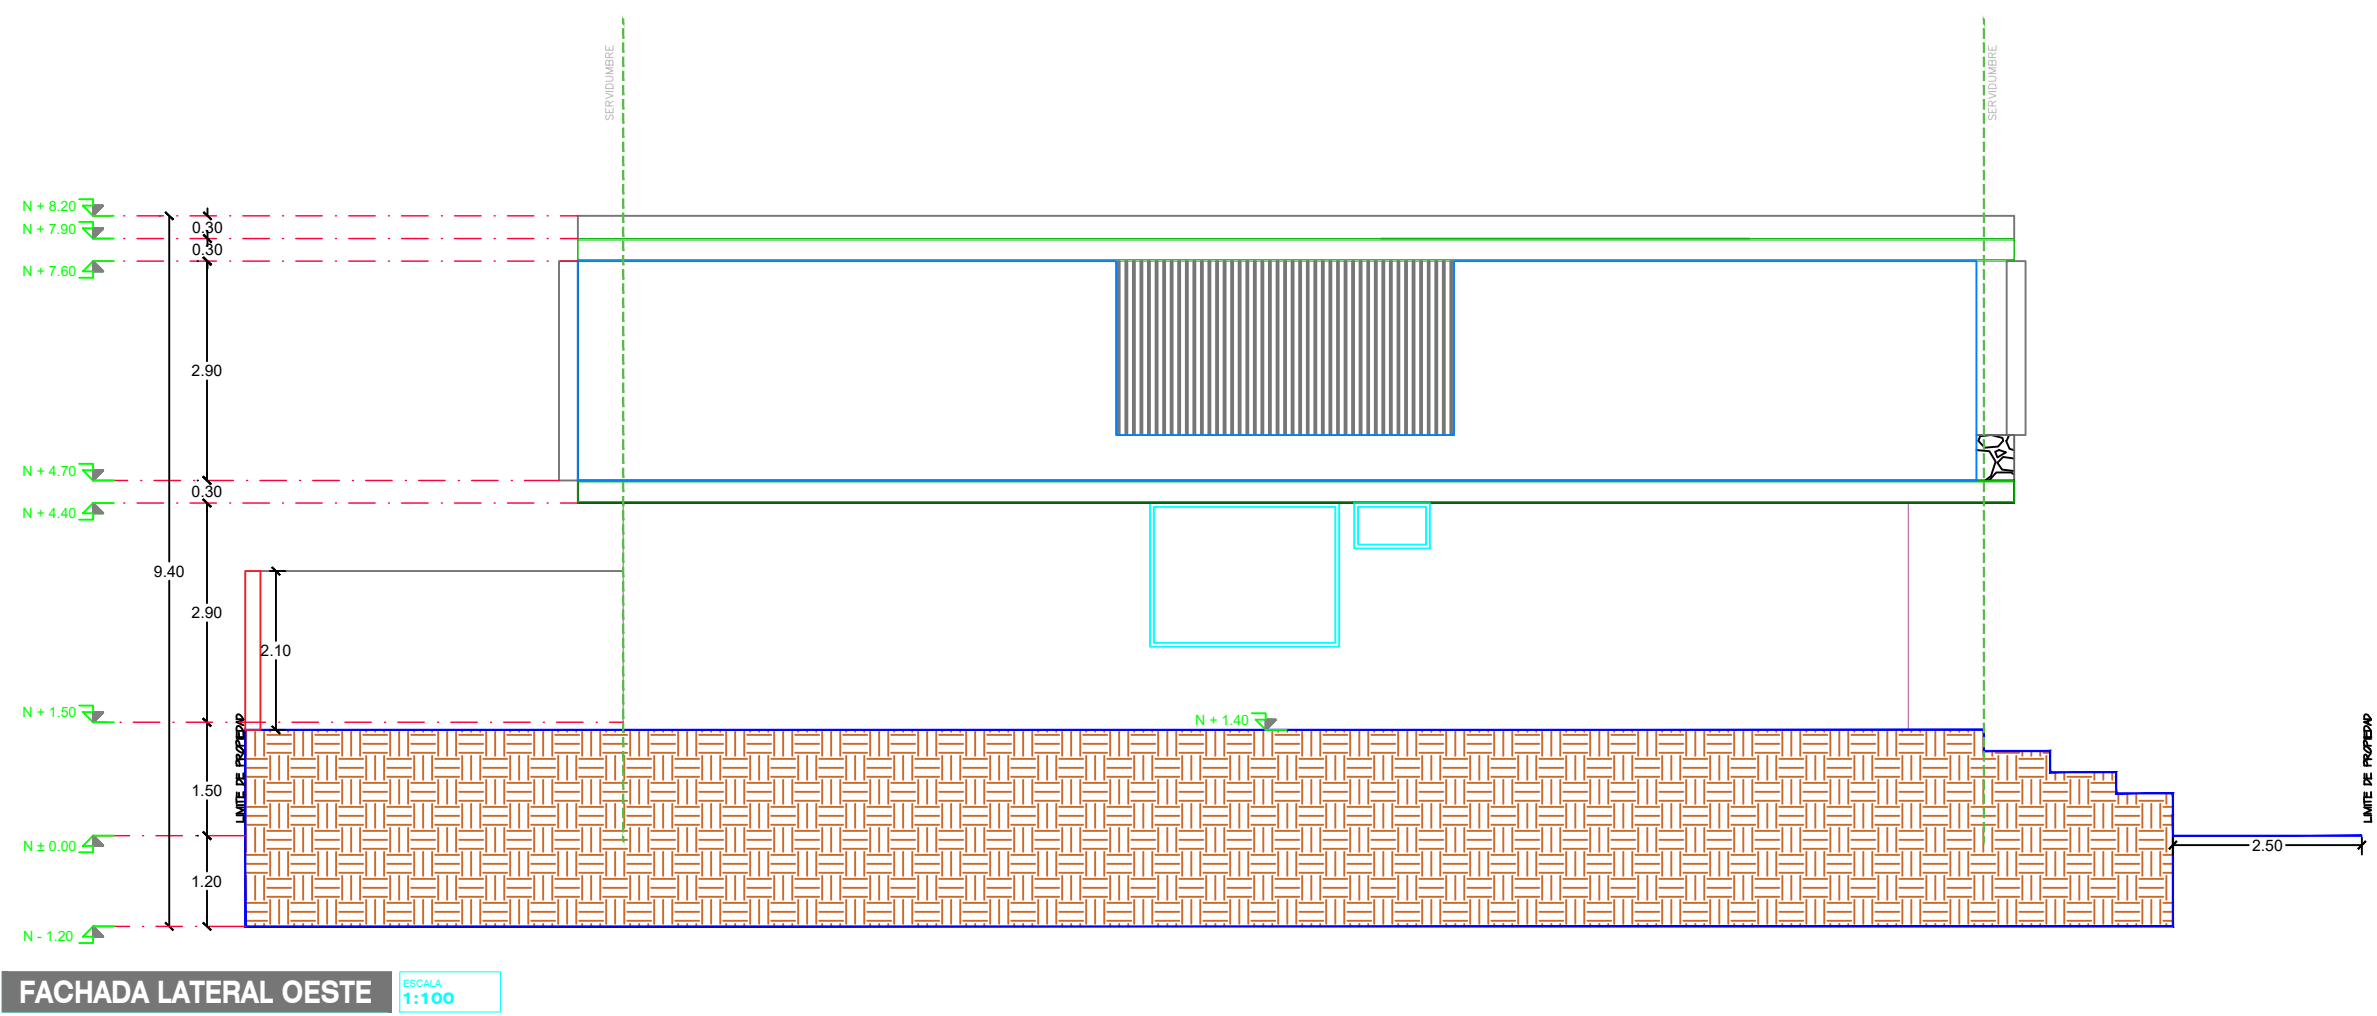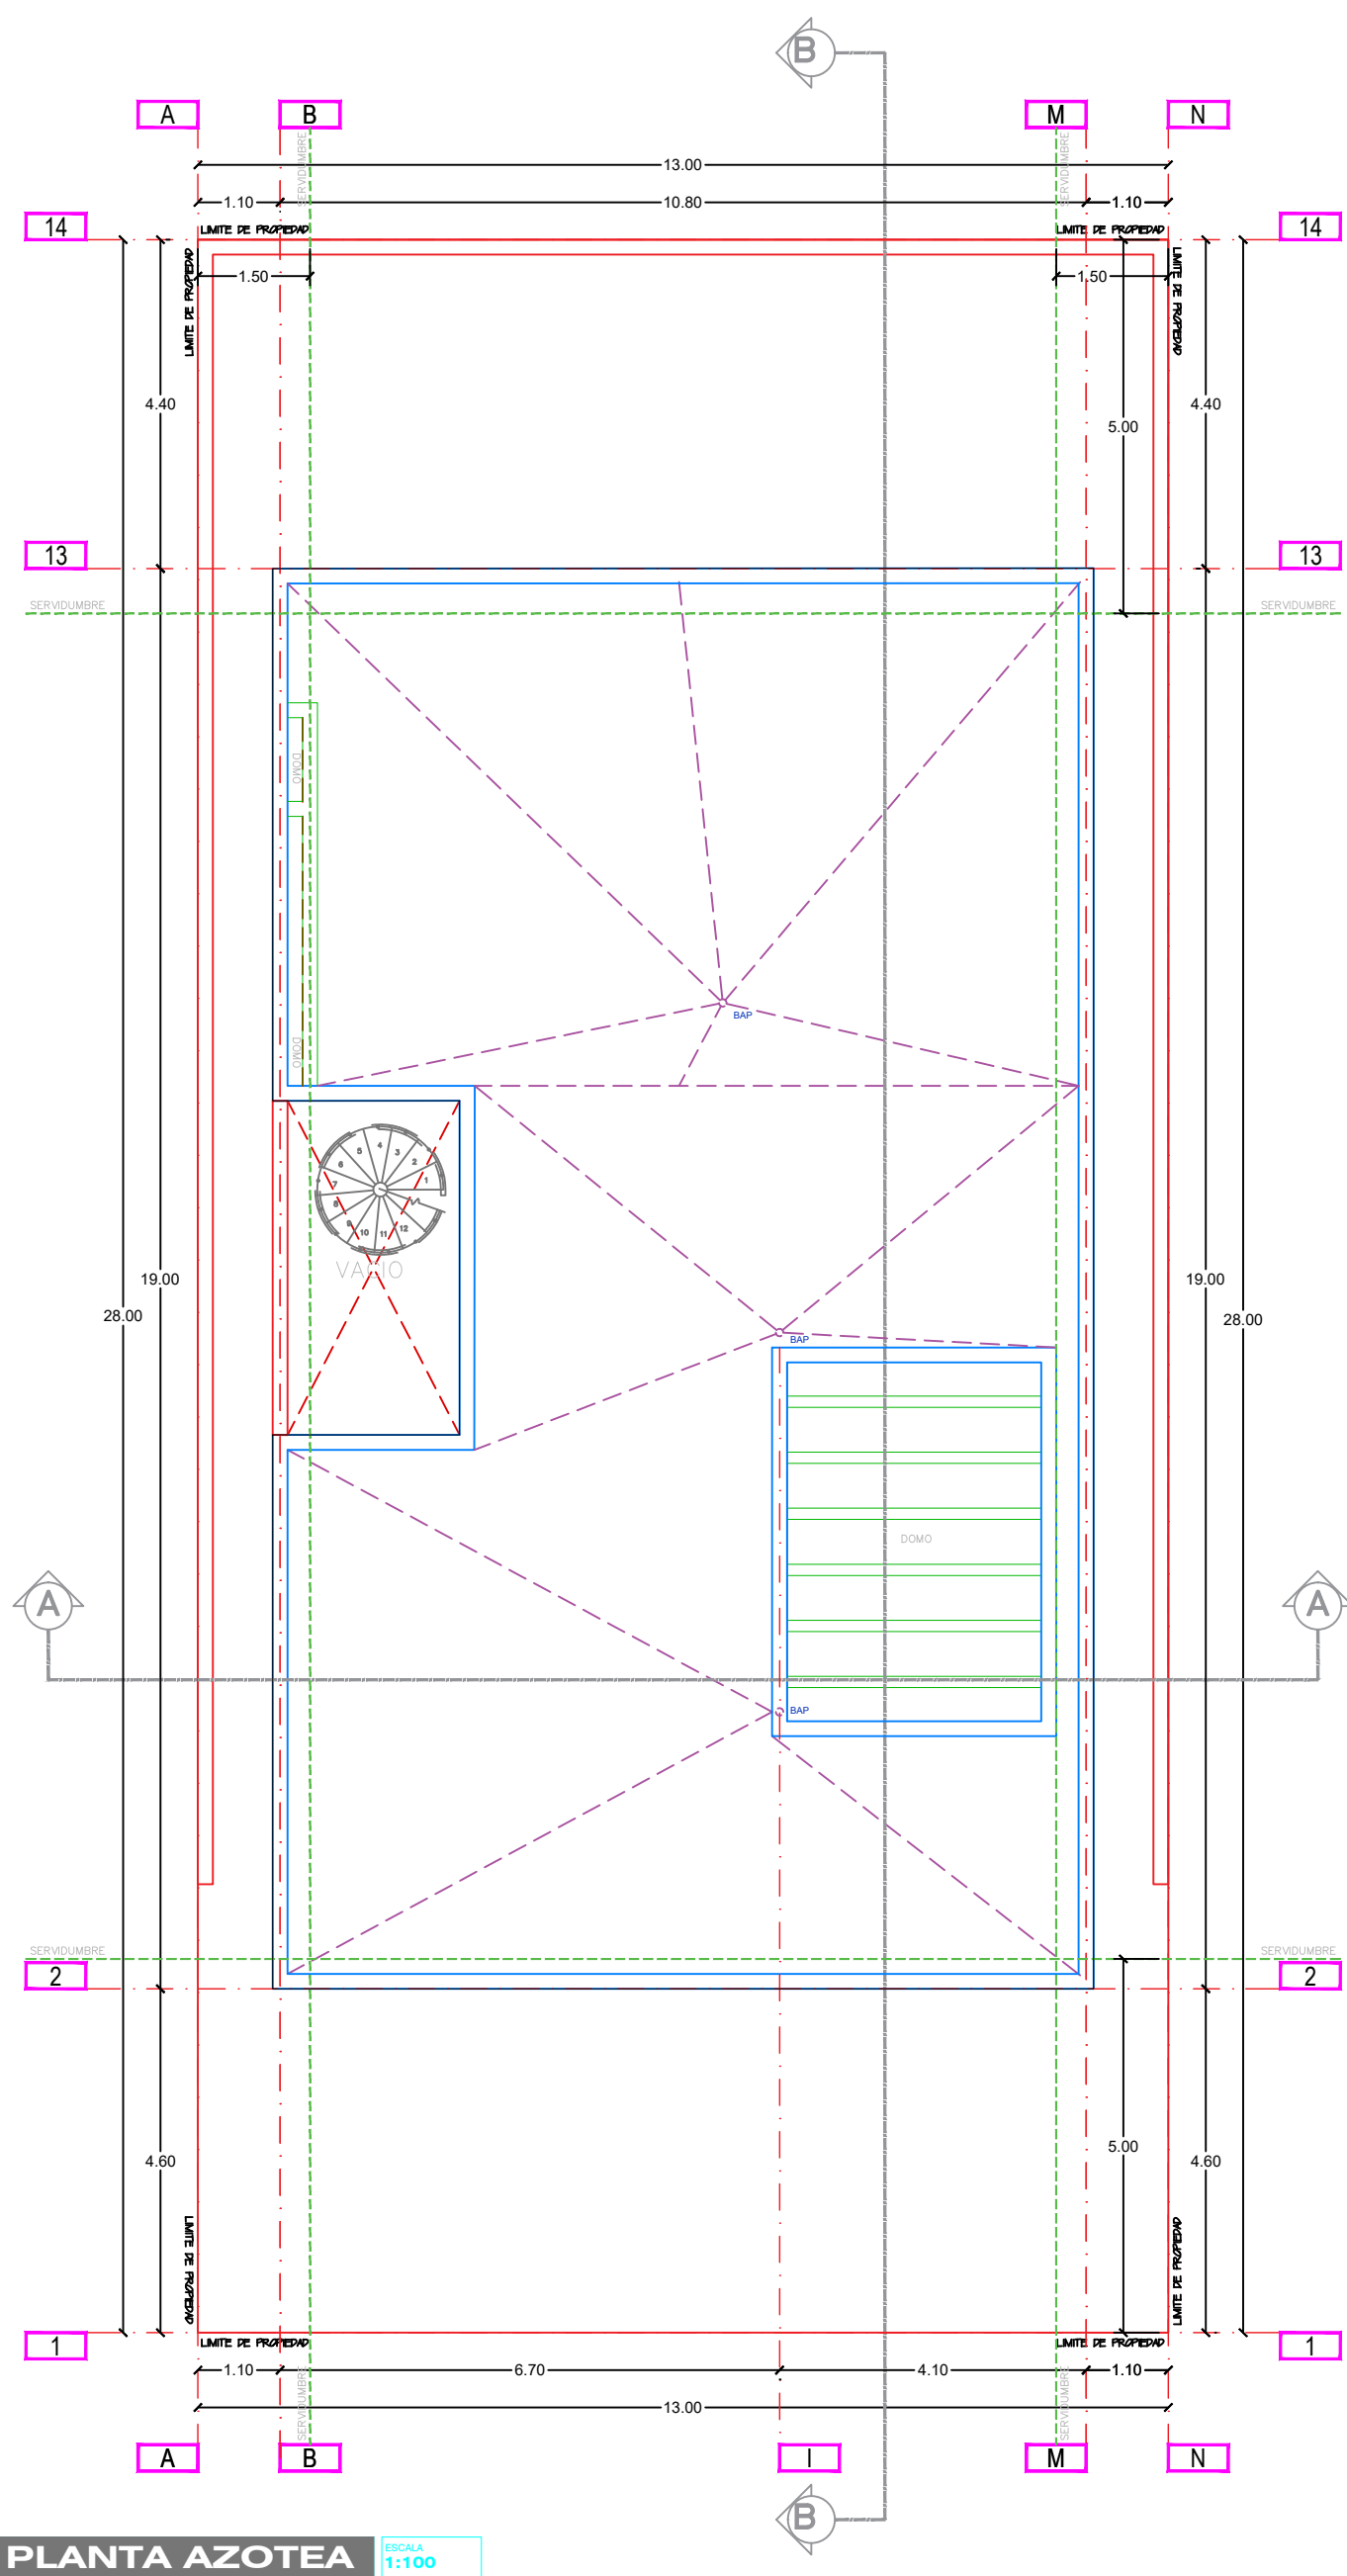


Permisos y  
Licencias de construcción  
Gestión Integral de la Ciudad

UBICACIÓN

MACRO:

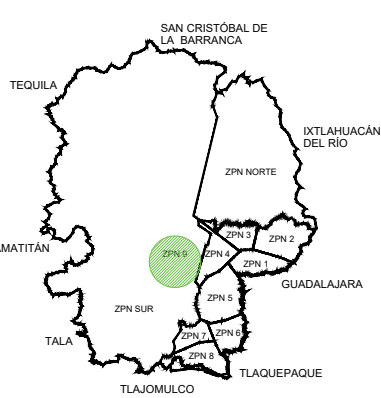

LOCALIZACIÓN MICRO:

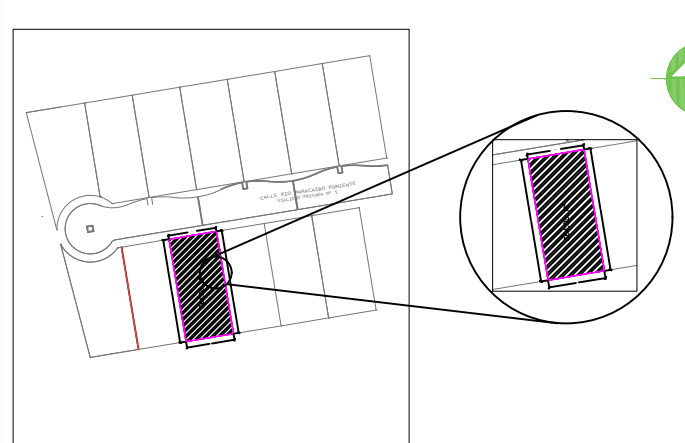

CUADRO DE ÁREAS

|                        | Unidad | Propuesto |
|------------------------|--------|-----------|
| SUPERFICIE DEL TERRENO | m2     | 364.00 m2 |
| SOTANO                 | m2     | 150.73 m2 |
| PLANTA BAJA            | m2     | 186.35 m2 |
| PLANTA ALTA            | m2     | 198.34 m2 |
| AZOTEA                 | m2     | —         |
| TOTAL                  | m2     | 535.42 m2 |
| BARDEO                 | ml     | 57.00 ml  |
| CISTERNA               | m3     | 10.00 m3  |

NOTA: CUALQUIER ELEMENTO CONSTRUCTIVO NO SEÑALADO DEBERÁ ANOTARSE EN ESTE RECUADRO.

COEFICIENTES

|            | C.O.S.      | C.U.S.      |
|------------|-------------|-------------|
| PERMITIDO  | 0.6 218 m2  | 1.2 436 m2  |
| PROYECTADO | 0.42 187 m2 | 1.06 385 m2 |

SIMBOLOGÍA

DATOS DEL PREDIO

|                                  |                       |    |
|----------------------------------|-----------------------|----|
| CALLE: General Río San Francisco |                       |    |
| NÚMERO:                          | CONDOMINIO: ARAUCA II |    |
| LOTE 182                         | MANZANA               | UP |
| COLONIA: ARAUCA II               |                       |    |

PROPIETARIO(S)

|                |
|----------------|
| DIETER BÜCHNER |
|----------------|

FIRMA

|                                         |
|-----------------------------------------|
| DIRECTOR RESPONSABLE EN PROYECTO Y OBRA |
| RICARDO ORTIZ FLORES                    |
| DRZ- 0424/2025                          |

FIRMA

|                           |
|---------------------------|
| DIBUJO: SYD CONSTRUCTORES |
|---------------------------|

|                                           |
|-------------------------------------------|
| TÍTULO                                    |
| CASA ARAUCA                               |
| CONTENIDO                                 |
| PLANTA AZOTEA, FACHADA LATERAL, SECCIONES |

|        |            |                  |
|--------|------------|------------------|
| ESCALA | FECHA      | NÚMERO DE LÁMINA |
| 1:100  | MARZO 2026 | 2/2              |