
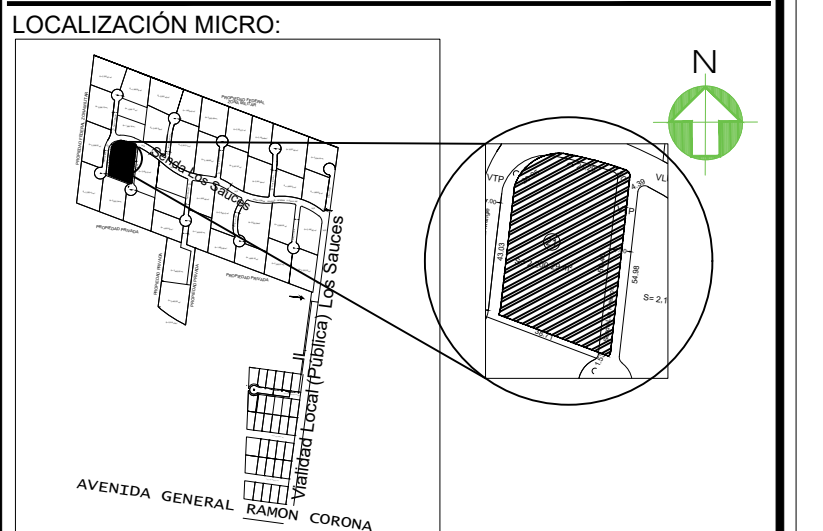


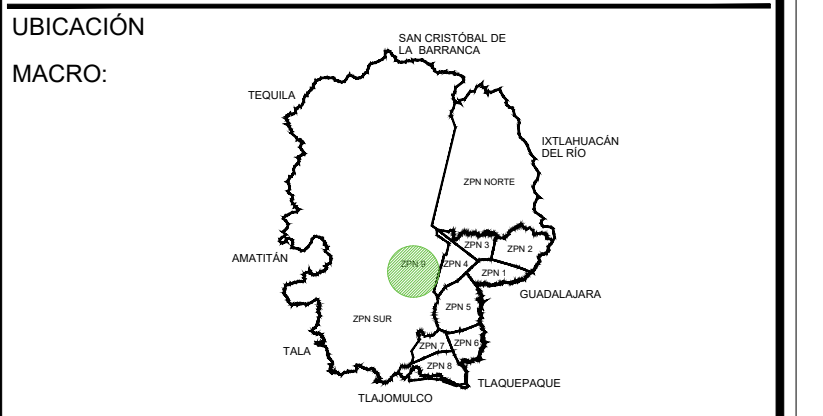

CUADRO DE ÁREAS			
	ACTUAL	PROPUESTO	
TERRENO	2200.29 m ²	2200.29 m ²	
PLANTA BAJA	595.59 m ²	752.83 m ²	
PLANTA ALTA	--- m ²	118.32 m ²	
TOTAL	595.59 m ²	871.15 m ²	
CUBIERTA LIGERA	15.16 m ²		

NOTA: CUALQUIER ELEMENTO CONSTRUCTIVO NO SEÑALADO DEBERÁ ANOTARSE EN ESTE RECUADRO.

COEFICIENTES			
	C.O.S.		C.U.S.
PERMITIDO	0.4	880m ²	0.7 1540m ²
PROYECTADO	0.34	752.8m ²	0.4 871.1m ²

SIMBOLOGÍA	
	AMPLIACION 275.46m ²
	DESMTAR 23.7m ²

DATOS DEL PREDIO			
CALLE: LOS SAUCES			
NÚMERO:	CONDominio: RANCHO LOS SAUCES		
LOTE 21	MANZANA	UP	

COLONIA:FRACC. LOS SAUCES

PROPIETARIO(S)	
GUILLERMO OROZCO VALENZUELA	

FIRMA
DIRECTOR RESPONSABLE EN PROYECTO Y OBRA
RICARDO ORTIZ FLORES
DRZ- 0424/2026

FIRMA
DIBUJO: SYD CONSTRUCTORES



TÍTULO
AMPLIACION SAUCES

CONTENIDO
PLANTA BAJA ESTADO ACTUAL

ESCALA	FECHA	NÚMERO DE
1:100	ABRIL 2026	LÁMINA:
		1/7



PLANTA BAJA ESTADO ACTUAL
ARQUITECTONICA
ESCALA 1:100

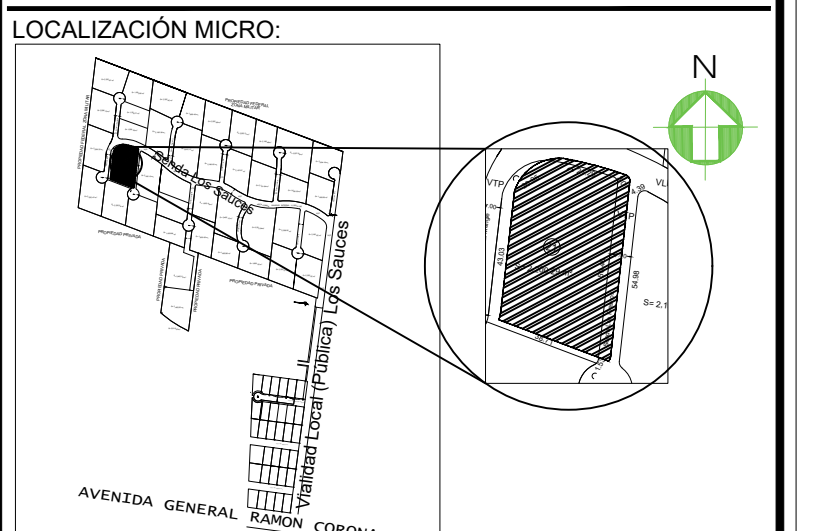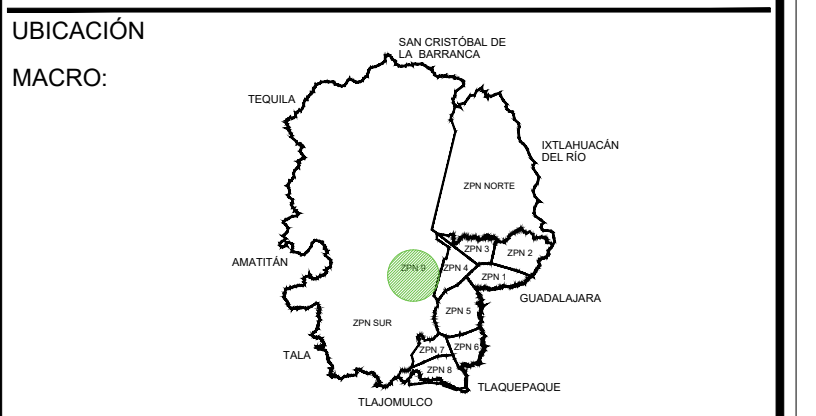

CUADRO DE ÁREAS			
TERRENO	ACTUAL	PROPUESTO	
PLANTA BAJA	595.59 m ²	752.83 m ²	
PLANTA ALTA	---	118.32 m ²	
TOTAL	595.59 m ²	871.15 m ²	
CUBIERTA LIGERA	15.16 m ²		

NOTA: CUALQUIER ELEMENTO CONSTRUCTIVO NO SEÑALADO DEBERÁ ANOTARSE EN ESTE RECUADRO.

COEFICIENTES				
	C.O.S.		C.U.S.	
PERMITIDO	0.4	880 m2	0.7	1540 m2
PROYECTADO	0.34	752.8m2	0.4	871.1m2

SIMBOLOGÍA	
AMPLIACION	275.46m ²
DESMONTAR	23.7m ²

DATOS DEL PREDIO	
CALLE: LOS SAUCES	
NÚMERO: 21	CONDominio: RANCHO LOS SAUCES
LOTE: 21	MANZANA: 1
COLONIA: FRACC. LOS SAUCES	UP: 1A

PROPIETARIO(S)	
GUILLERMO OROZCO VALENZUELA	
PROPUESTO	
757.49 m ²	
FIRMA: 15.32 m ²	
DIRECTOR RESPONSABLE EN PROYECTO Y OBRA	
RICARDO ORTIZ FLORES	
CUBIERTA LIGERA 15.16 m ²	
DRZ= 0424/2026	


FIRMA	
DIBUJO: SYD CONSTRUCTORES	
TÍTULO	AMPLIACION SAUCES
CONTENIDO	PLANTA BAJA AMPLIACION
AMPLIACION	275.46 m ²
DESMONTAR	23.7 m ²
ESCALA	1:100
FECHA	26 ABRIL 2026
NÚMERO DE LÁMINA	2/7




PLANTA BAJA ESTADO PROPUESTO
ARQUITECTONICA
ESCALA 1:100



UBICACIÓN

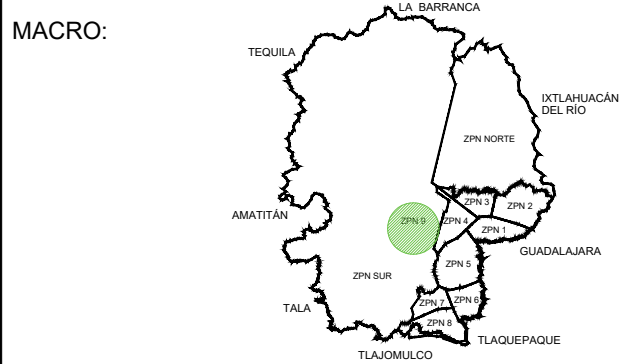

LOCALIZACIÓN MICRO:

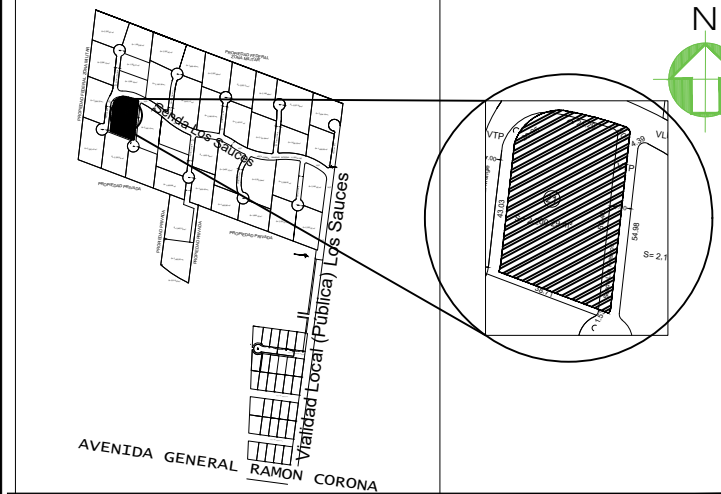

CUADRO DE ÁREAS

	ACTUAL	PROPUESTO
TERRENO	2200.29 m ²	2200.29 m ²
PLANTA BAJA	595.59 m ²	752.83 m ²
PLANTA ALTA	---	118.32 m ²
TOTAL	595.59 m ²	871.15 m ²
CUBIERTA LIGERA	15.16 m ²	

NOTA: CUALQUIER ELEMENTO CONSTRUCTIVO NO SEÑALADO DEBERÁ ANOTARSE EN ESTE RECUADRO.

COEFICIENTES

	C.O.S.	C.U.S.
PERMITIDO	0.4 880 m ²	0.7 1540 m ²
PROYECTADO	0.34 752.8m ²	0.4 871.1m ²

SIMBOLOGÍA

AMPLIACION	275.46m ²
DESMONTAR	23.7m ²

DATOS DEL PREDIO

CALLE: LOS SAUCES		
NÚMERO:	CONDominio: RANCHO LOS SAUCES	
LOTE 21	MANZANA	UP
COLONIA: FRACC. LOS SAUCES		

PROPIETARIO(S)

GUILLERMO OROZCO VALENZUELA

FIRMA

DIRECTOR RESPONSABLE EN PROYECTO Y OBRA

RICARDO ORTIZ FLORES

DRZ- 0424/2026

FIRMA

DIBUJO: SYD CONSTRUCTORES

TÍTULO


AMPLIACION SAUCES

CONTENIDO

PLANTA ALTA ESTADO ACTUAL

ESCALA	FECHA	NÚMERO DE LÁMINA
--------	-------	------------------

1:100	ABRIL 2026	3/7
-------	------------	-----

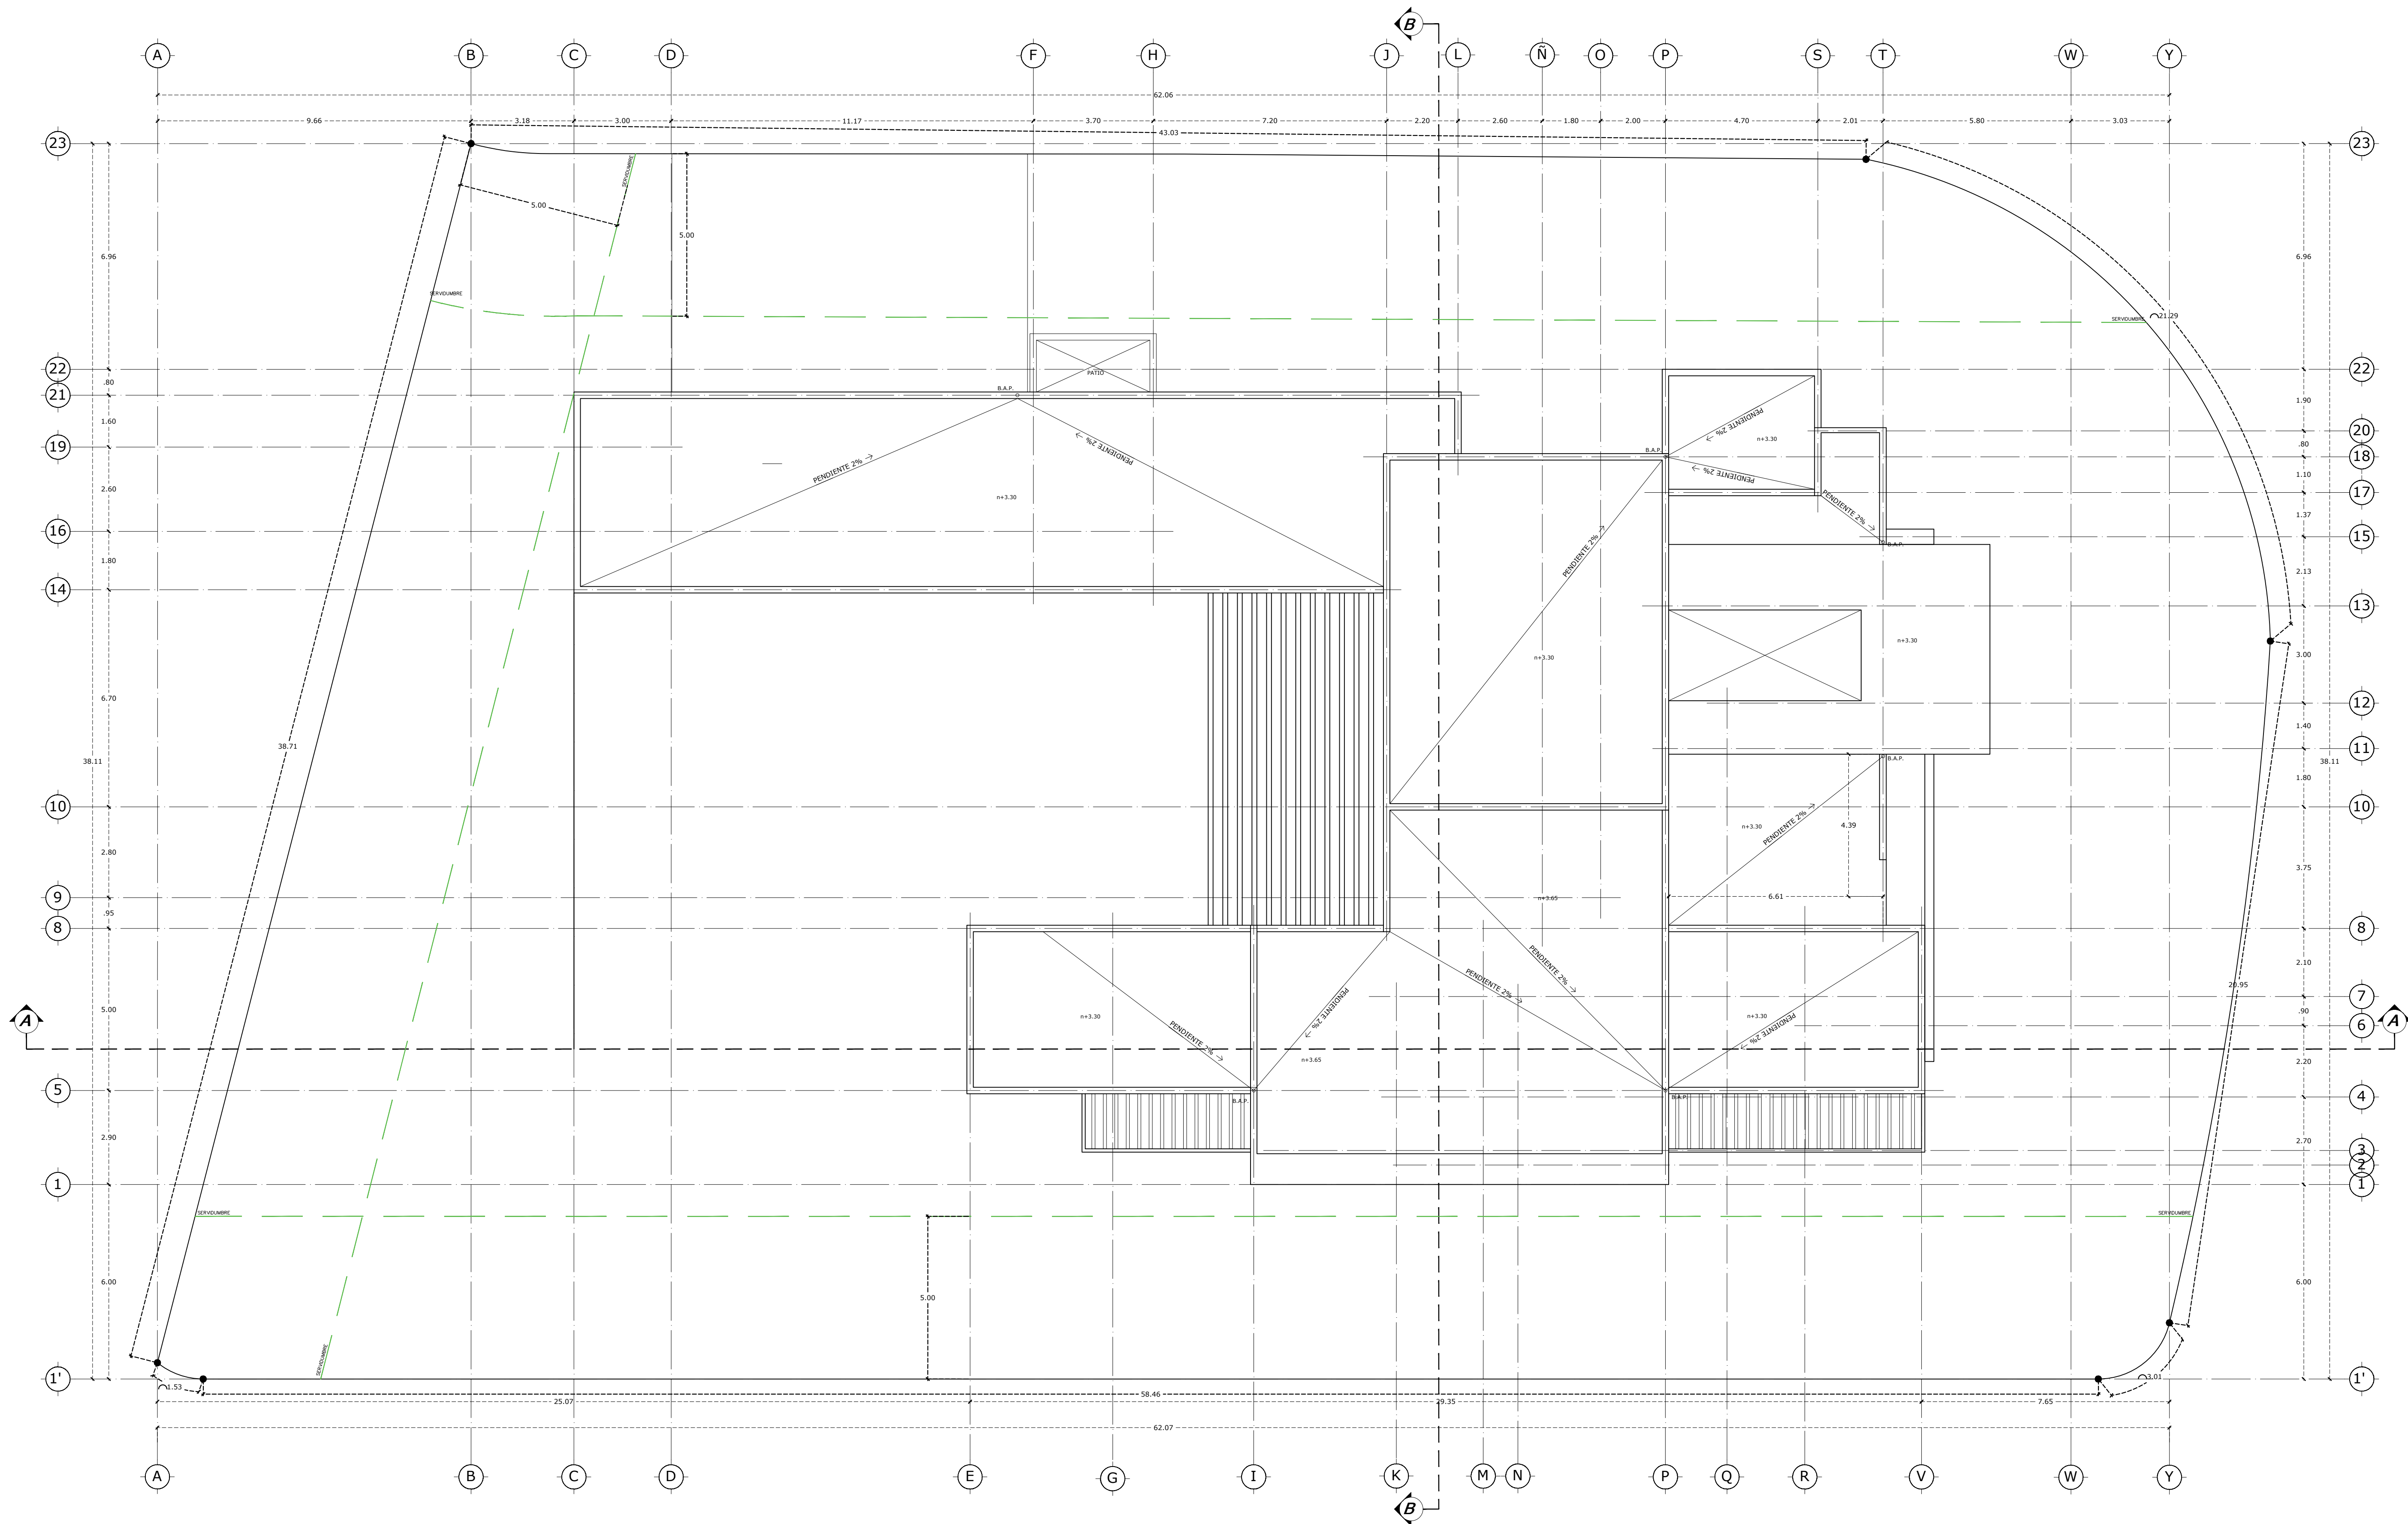


PLANTA DE ALTA ESTADO ACTUAL
ARQUITECTONICA
ESCALA 1:100




Permisos y
Licencias de construcción
Gestión Integral de la Ciudad

UBICACIÓN

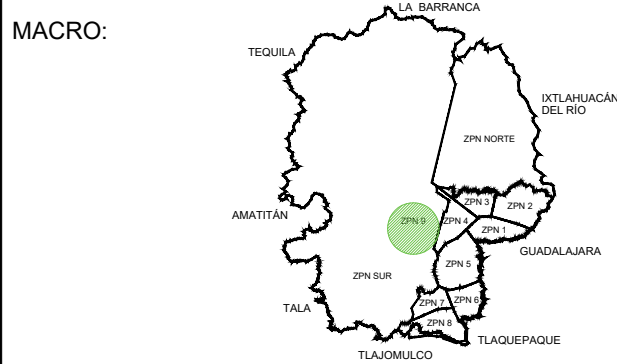

LOCALIZACIÓN MICRO:

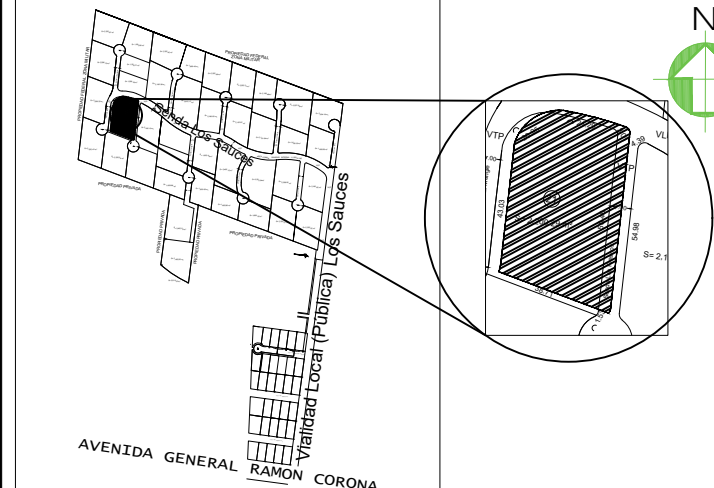

CUADRO DE ÁREAS

	ACTUAL	PROPUESTO
TERRENO	2200.29 m ²	2200.29 m ²
PLANTA BAJA	595.59 m ²	752.83 m ²
PLANTA ALTA	---	118.32 m ²
TOTAL	595.59 m ²	871.15 m ²
CUBIERTA LIGERA	15.16 m ²	

NOTA: CUALQUIER ELEMENTO CONSTRUCTIVO NO SEÑALADO DEBERÁ ANOTARSE EN ESTE RECUADRO.

COEFICIENTES

	C.O.S.	C.U.S.
PERMITIDO	0.4 880 m ²	0.7 1540 m ²
PROYECTADO	0.34 752.8m ²	0.4 871.1m ²

SIMBOLOGÍA

AMPLIACION	275.46m ²
DESMONTAR	23.7m ²

DATOS DEL PREDIO

CALLE: LOS SAUCES		
NÚMERO:	CONDominio: RANCHO LOS SAUCES	
LOTE 21	MANZANA	UP
COLONIA: FRACC. LOS SAUCES		

PROPIETARIO(S)

GUILLERMO OROZCO VALENZUELA

FIRMA

DIRECTOR RESPONSABLE EN PROYECTO Y OBRA

RICARDO ORTIZ FLORES

DRZ- 0424/2026

FIRMA

DIBUJO: SYD CONSTRUCTORES

TÍTULO

AMPLIACION SAUCES

CONTENIDO

PLANTA ALTA AMPLIACION

ESCALA


1:100

FECHA



ABRIL 2026

NÚMERO DE LÁMINA

4/7

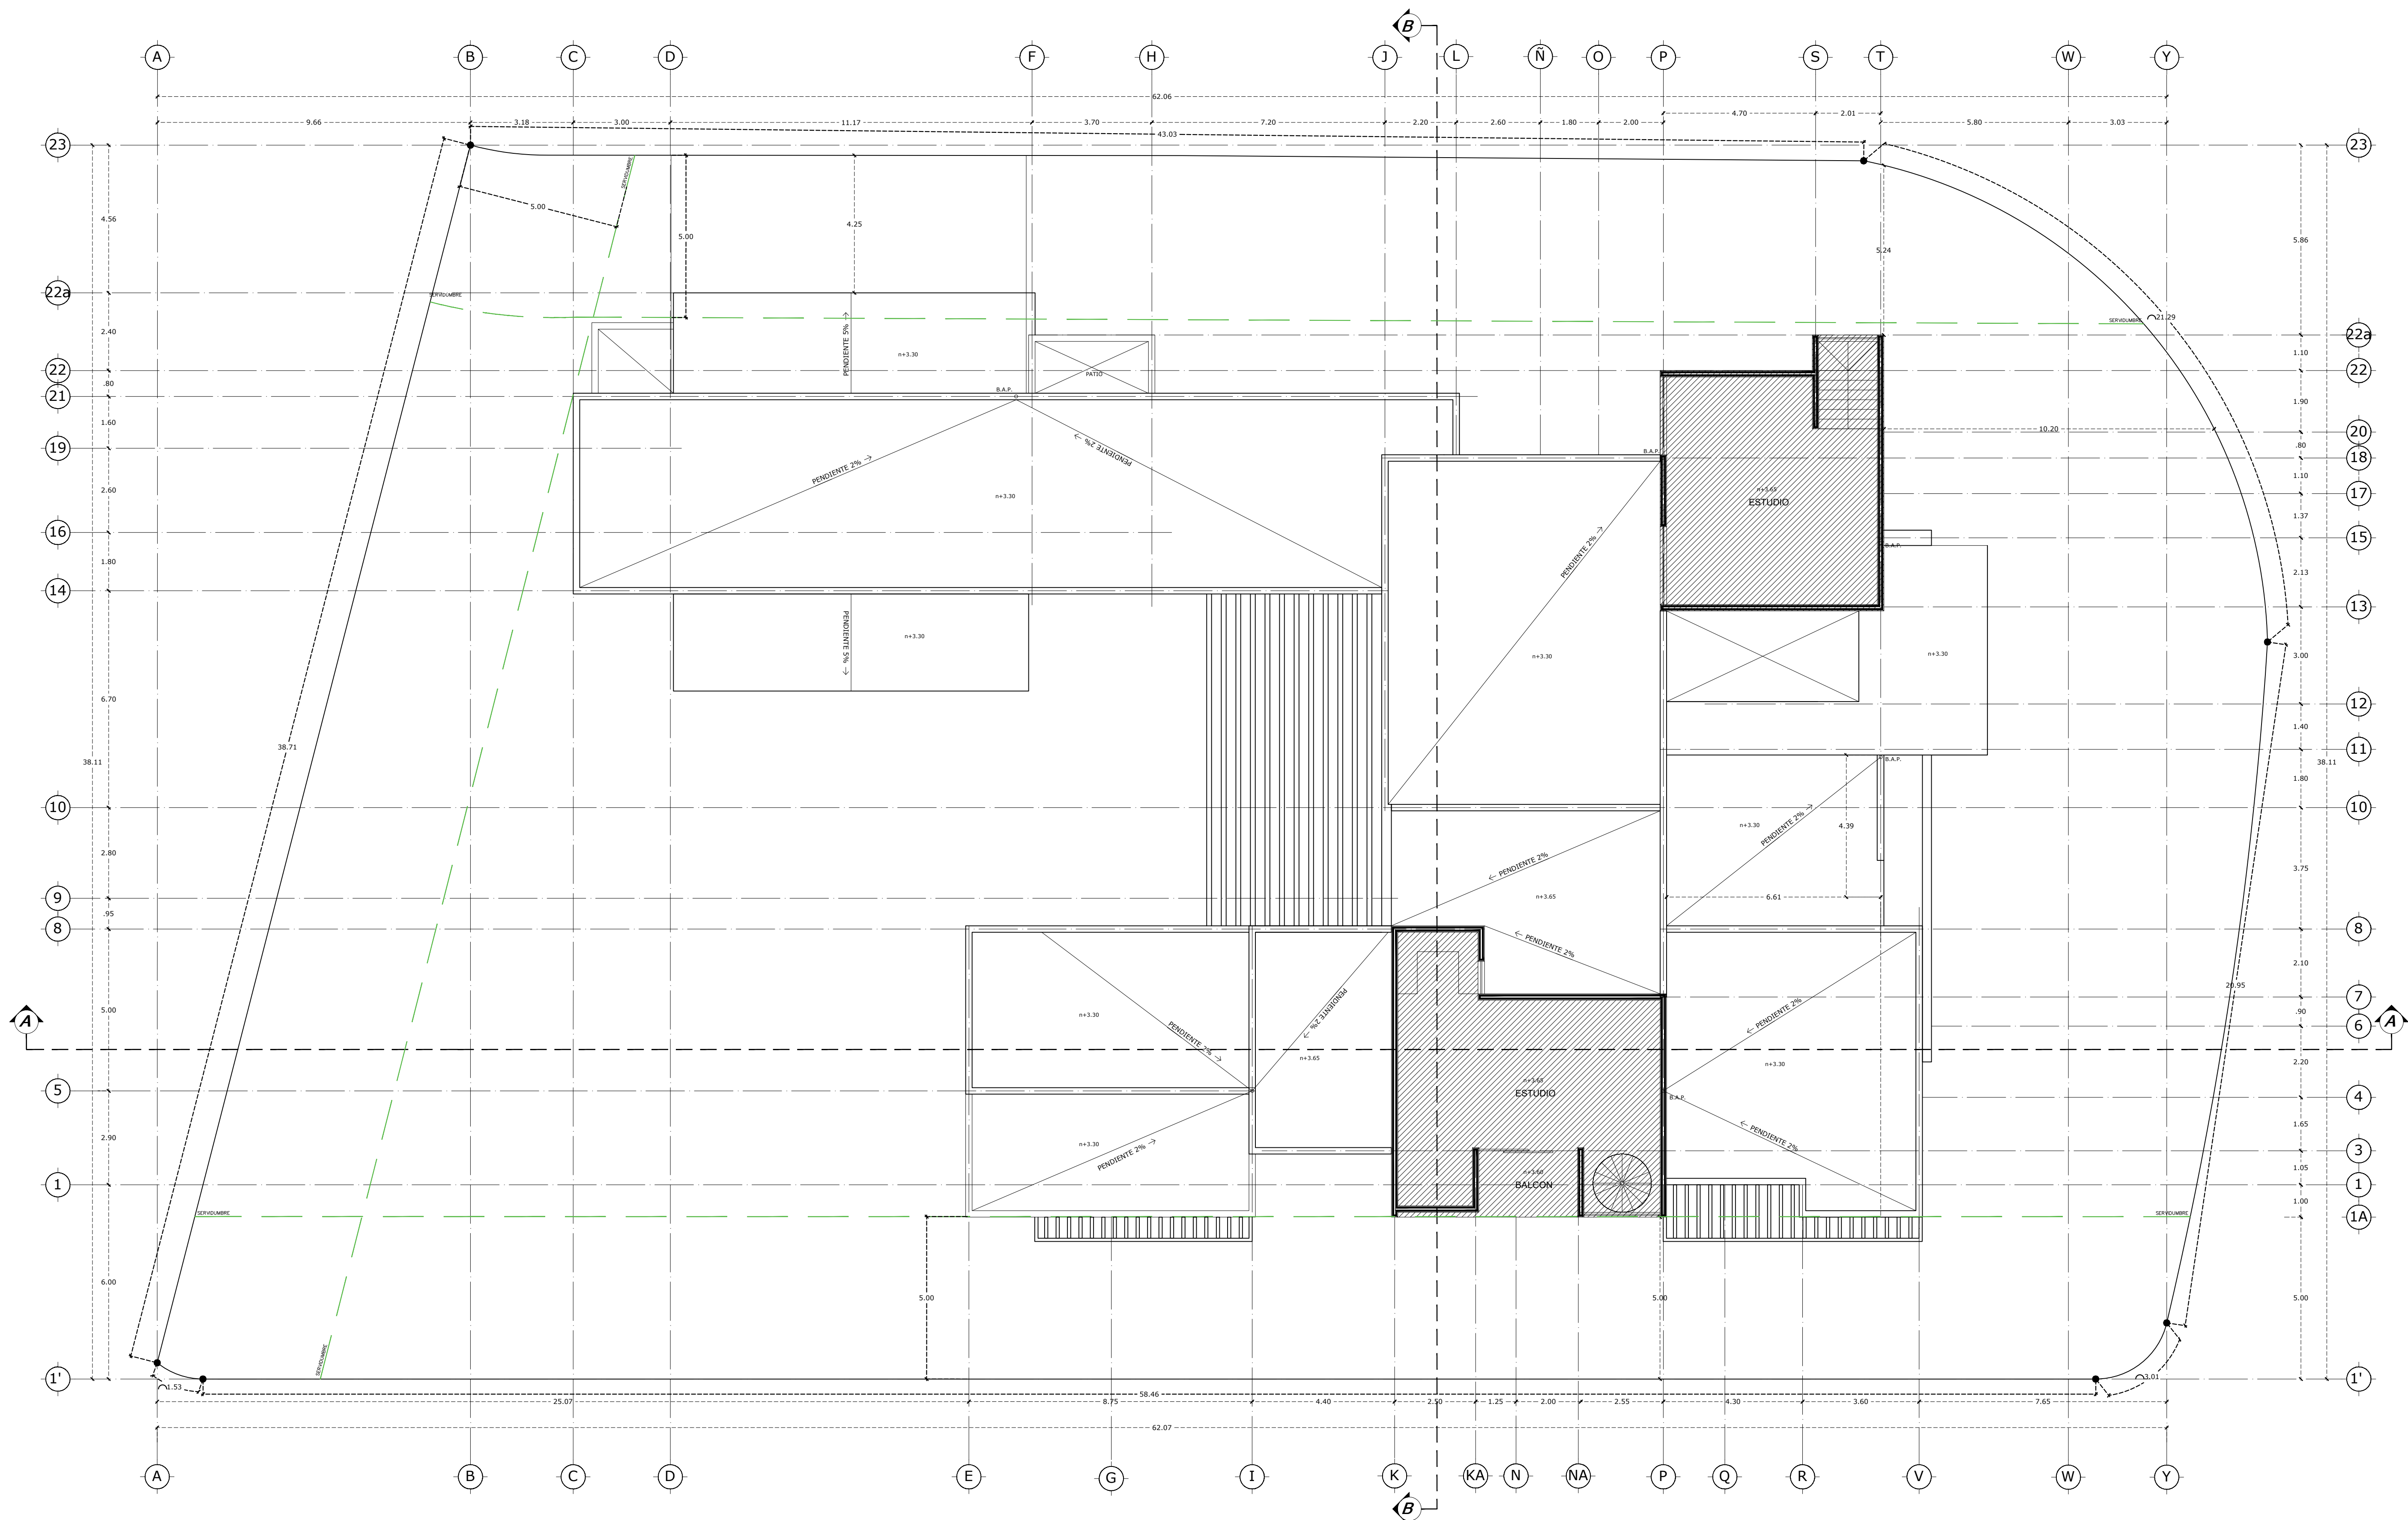

PLANTA ALTA ESTADO PROPUESTO
ARQUITECTONICA
ESCALA 1:100

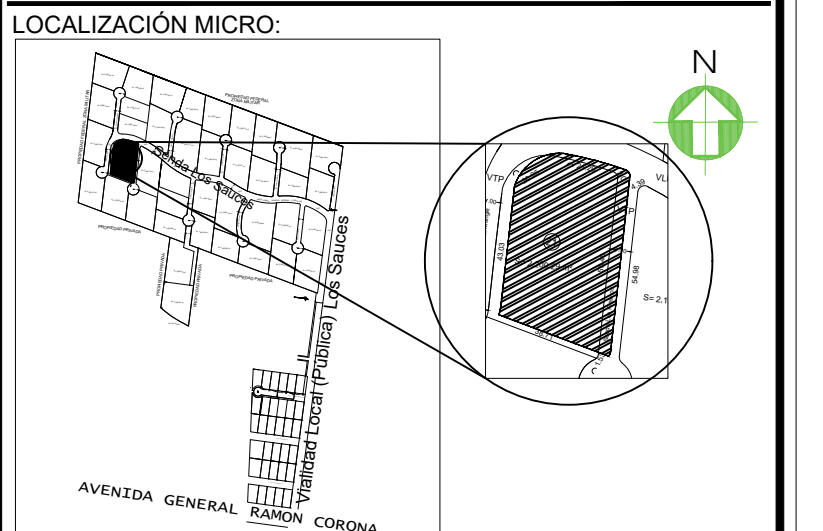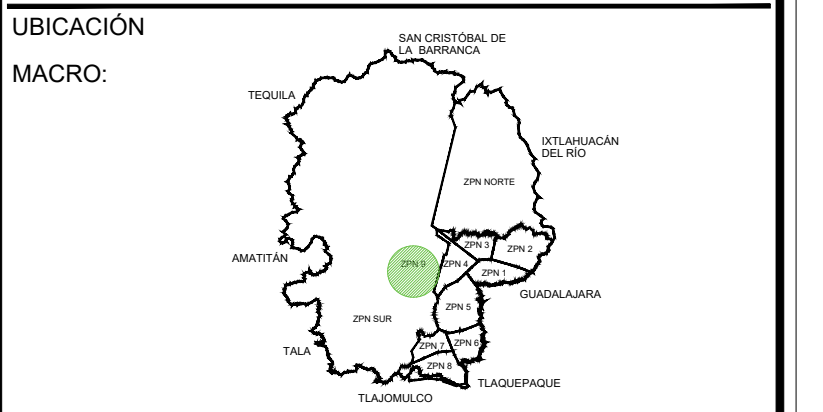

CUADRO DE ÁREAS			
	ACTUAL	PROPUESTO	
TERRENO	2200.29 m ²	2200.29 m ²	
PLANTA BAJA	595.59 m ²	752.83 m ²	
PLANTA ALTA	---	118.32 m ²	
TOTAL	595.59 m ²	871.15 m ²	
CUBIERTA LIGERA	15.16 m ²		

NOTA: CUALQUIER ELEMENTO CONSTRUCTIVO NO SEÑALADO DEBERÁ ANOTARSE EN ESTE RECUADRO.

COEFICIENTES			
	C.O.S.		C.U.S.
PERMITIDO	0.4	880 m ²	0.7 1540 m ²
PROYECTADO	0.34	752.8m ²	0.4 871.1m ²

SIMBOLOGÍA	
	AMPLIACION 275.46m ²
	DESMONTAR 23.7m ²

DATOS DEL PREDIO	
CALLE: LOS SAUCES	
NÚMERO:	CONDominio: RANCHO LOS SAUCES
LOTE 21	MANZANA UP
COLONIA: FRACC. LOS SAUCES	

PROPIETARIO(S)	
GUILLERMO OROZCO VALENZUELA	


FIRMA	
DIRECTOR RESPONSABLE EN PROYECTO Y OBRA	
RICARDO ORTIZ FLORES	
DRZ- 0424/2026	

FIRMA	
DIBUJO: SYD CONSTRUCTORES	

TÍTULO	
AMPLIACION SAUCES	

CONTENIDO	
PLANTA AZOTEA AMPLIACION	


ESCALA	FECHA	NÚMERO DE LÁMINA
1:100	ABRIL 2026	5/7

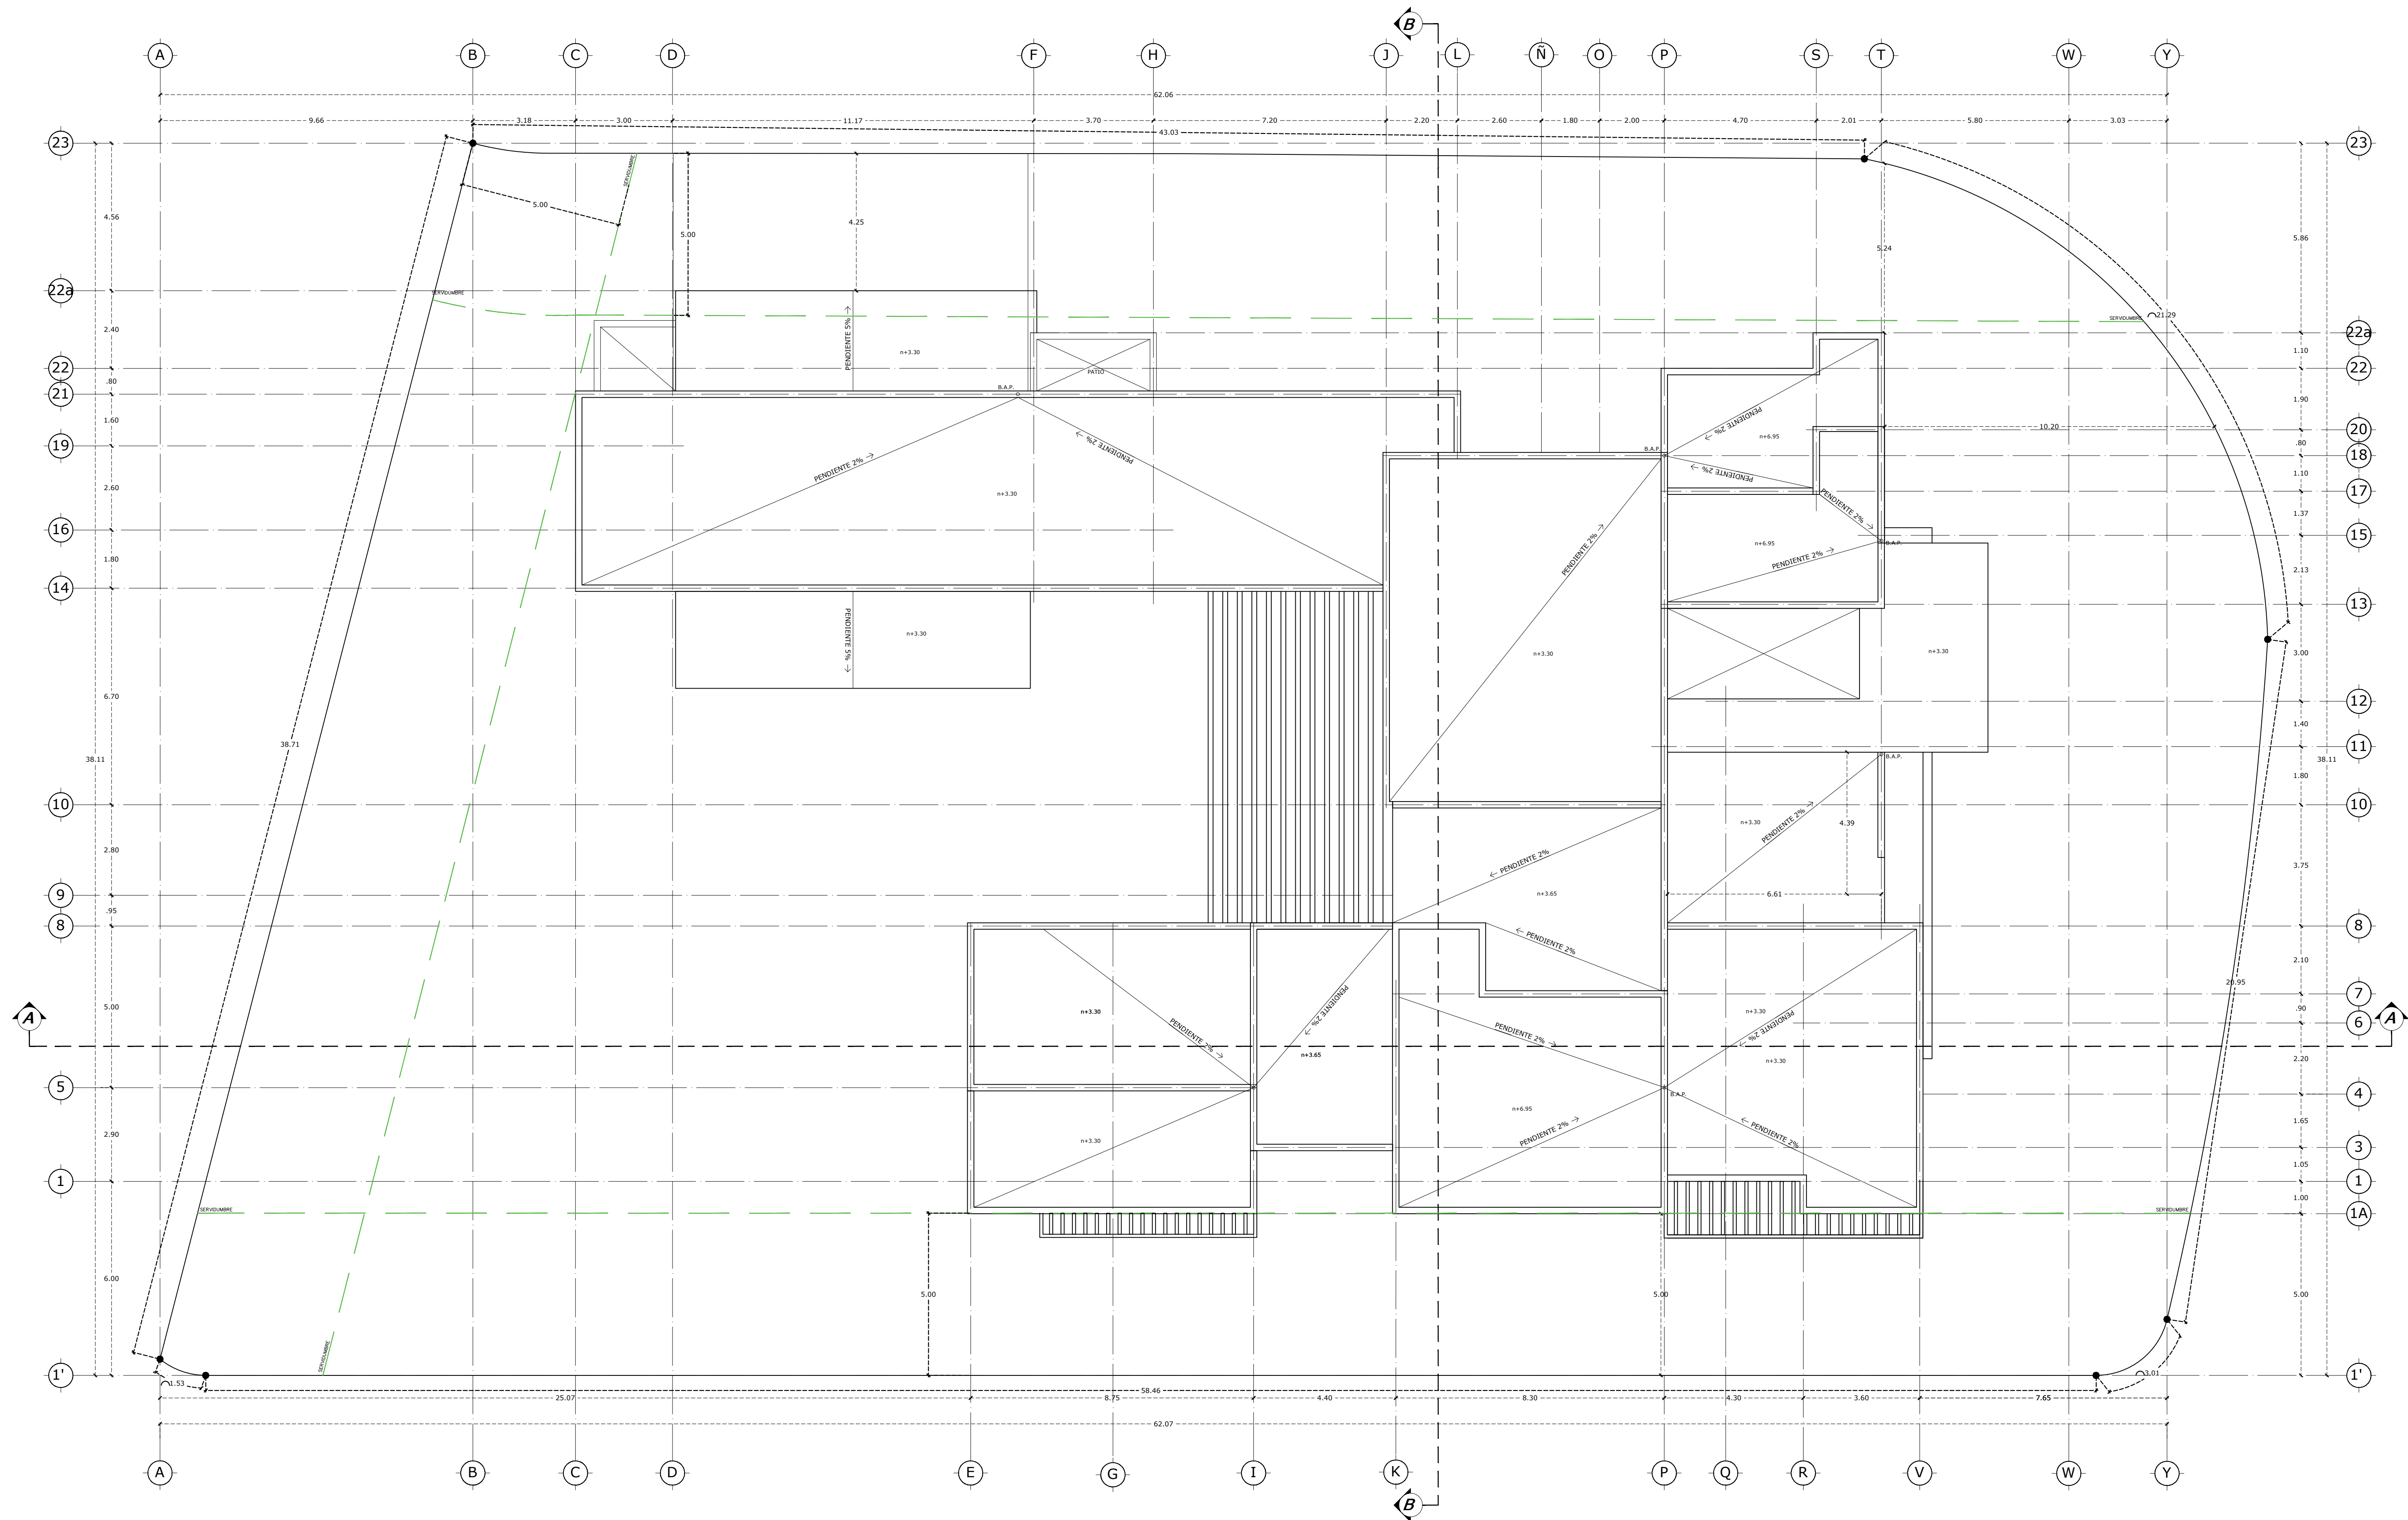


PLANTA DE AZOTEA ESTADO PROPUESTO
ARQUITECTÓNICA
ESCALA 1:100



UBICACIÓN

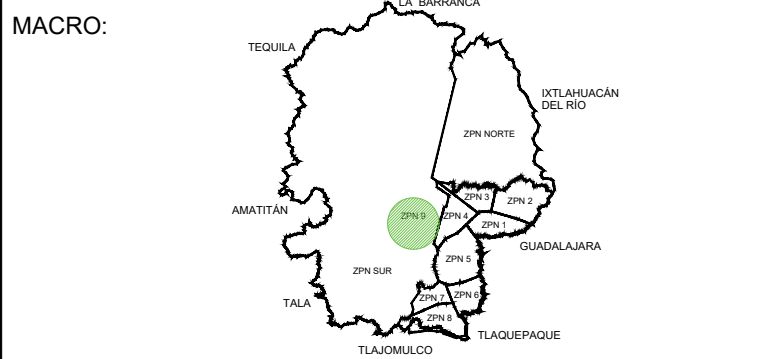

LOCALIZACIÓN MICRO:

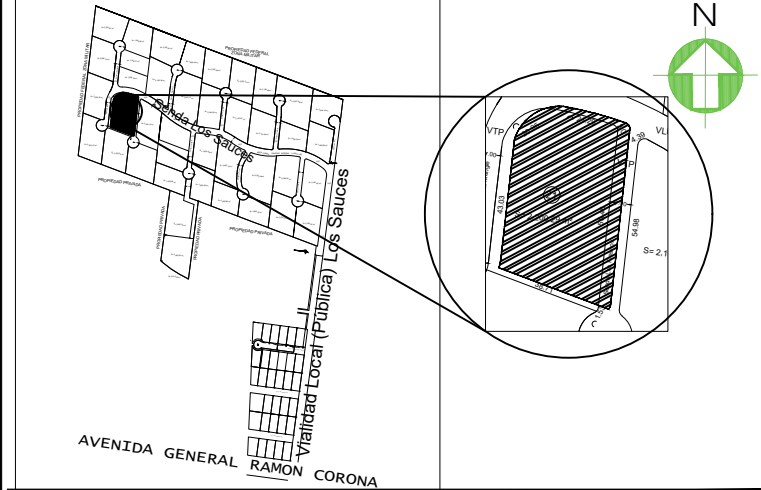

CUADRO DE ÁREAS

	ACTUAL	PROPUESTO
TERRENO	2200.29 m2	2200.29 m2
PLANTA BAJA	595.59 m2	752.83 m2
PLANTA ALTA	--- m2	118.32 m2
TOTAL	595.59 m2	871.15 m2
CUBIERTA LIGERA	15.16 m2	

NOTA: CUALQUIER ELEMENTO CONSTRUCTIVO NO SEÑALADO DEBERÁ ANOTARSE EN ESTE RECUADRO.

COEFICIENTES

	C.O.S.	C.U.S.
PERMITIDO	0.4 880 m2	0.7 1540 m2
PROYECTADO	0.34 752.8m2	0.4 871.1m2

SIMBOLOGÍA

AMPLIACION	272.46m2
DESMONTAR	23.7m2

DATOS DEL PREDIO

CALLE: LOS SAUCES		
NÚMERO:	CONDominio: RANCHO LOS SAUCES	
LOTE 21	MANZANA	UP

COLONIA:FRACC. LOS SAUCES

PROPIETARIO(S)

GUILLERMO OROZCO VALENZUELA

FIRMA

DIRECTOR RESPONSABLE EN PROYECTO Y OBRA
RICARDO ORTIZ FLORES
DRZ- 0424/2026


FIRMA

DIBUJO: SYD CONSTRUCTORES


TÍTULO
AMPLIACION SAUCES

CONTENIDO
SECCIONES, ALZADOS


ESCALA	FECHA	NÚMERO DE LÁMINA
1:100	ABRIL 2026	6/7

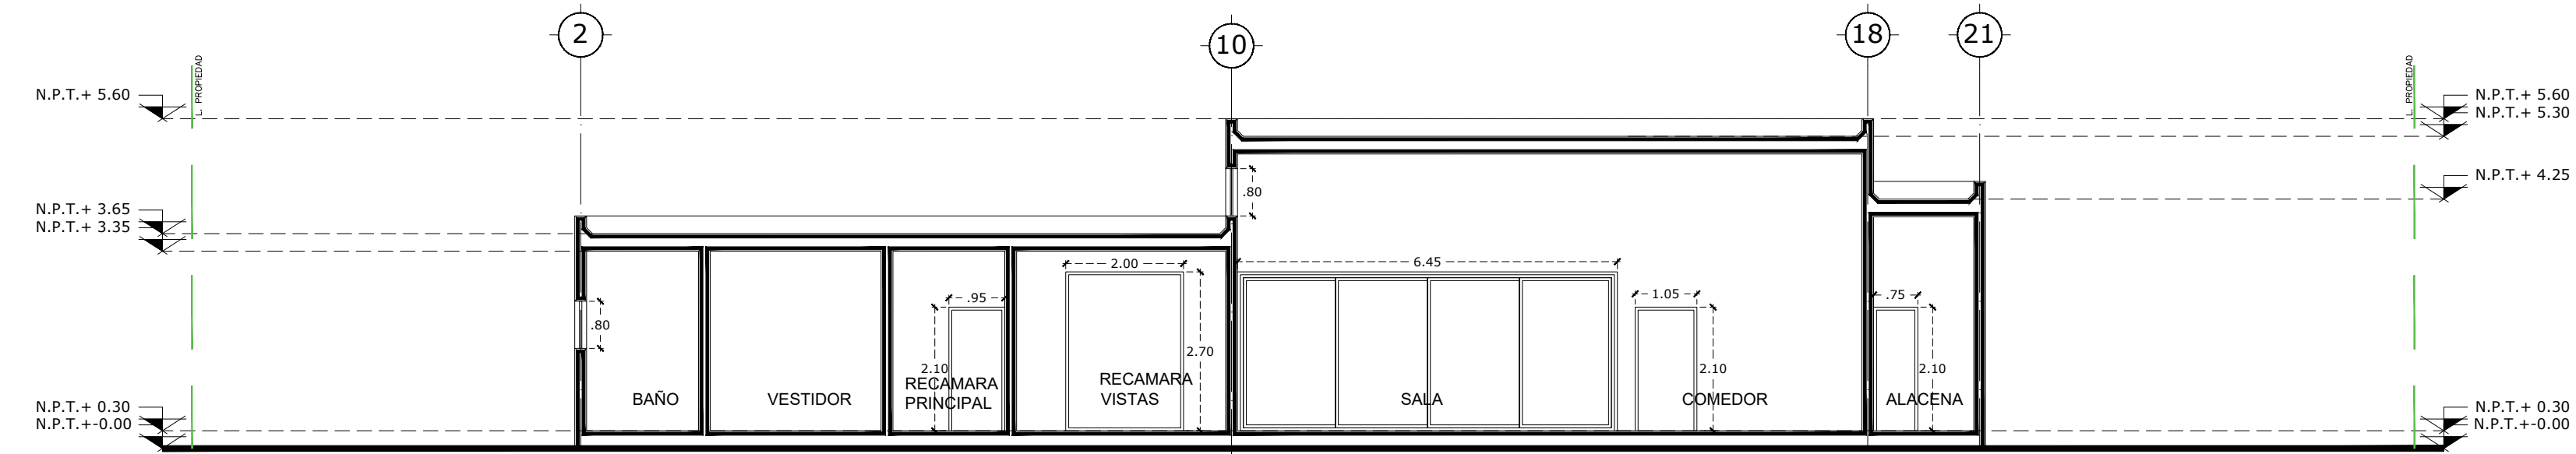


SECCION B-B
TRANSVERSAL ESTADO ACTUAL
ESCALA 1 : 100

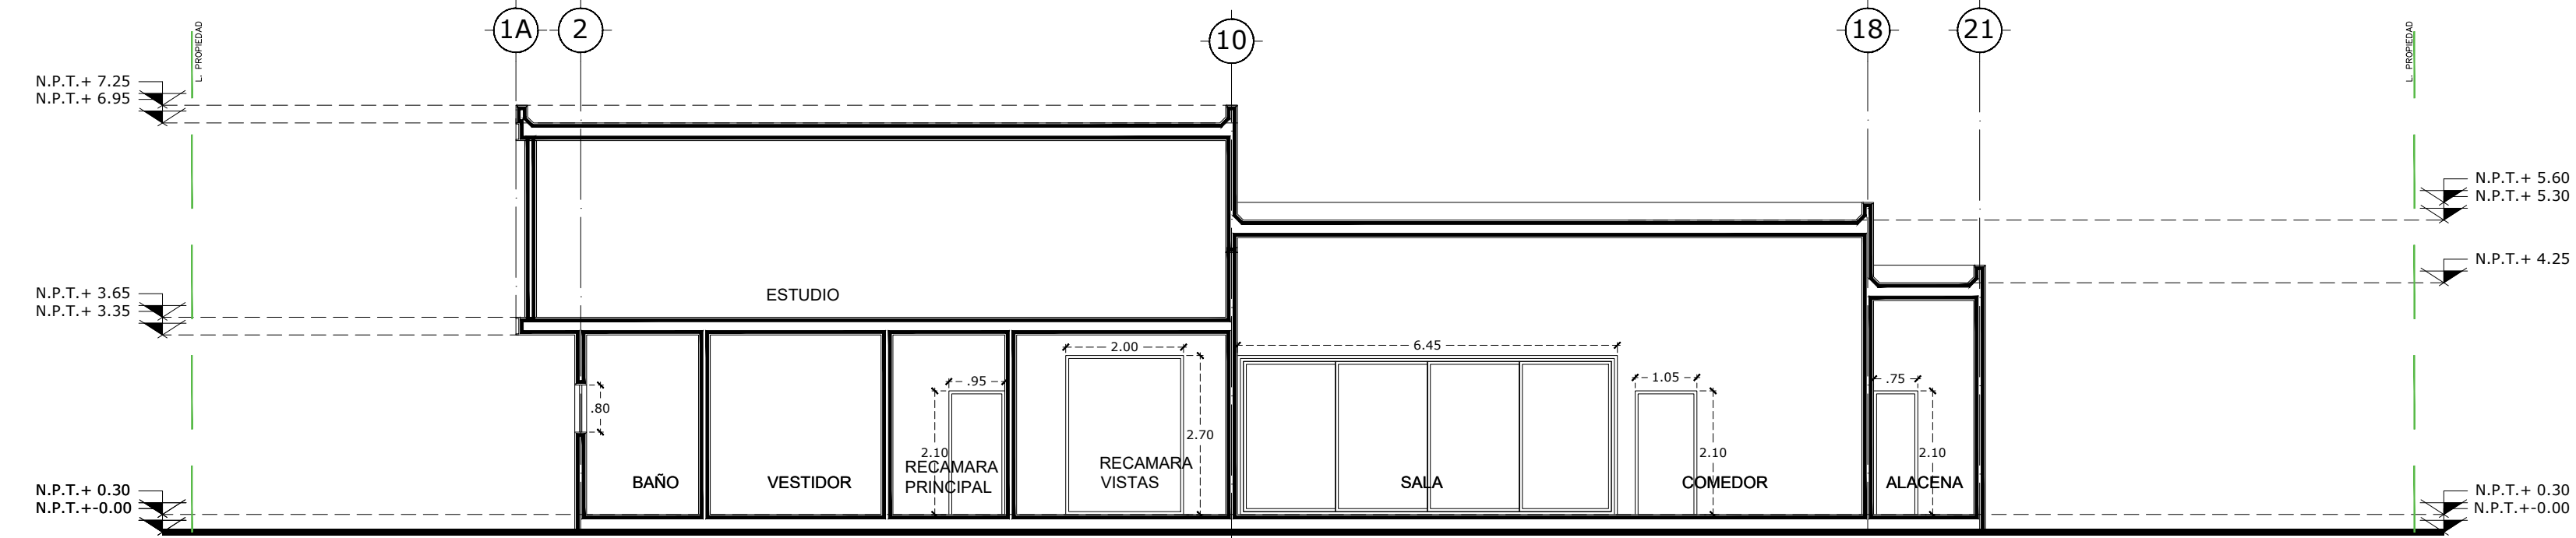


SECCION B-B
TRANSVERSAL ESTADO PROPUESTO
ESCALA 1 : 100

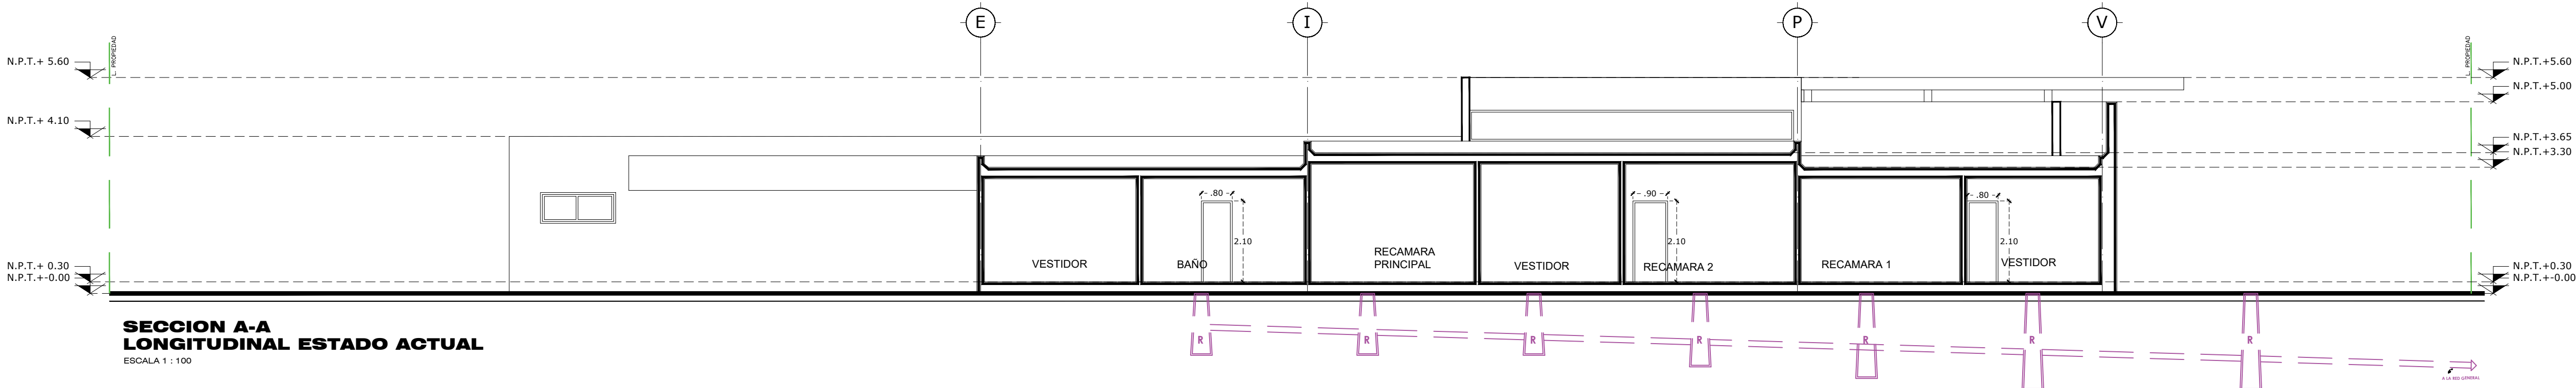

SECCION A-A
LONGITUDINAL ESTADO ACTUAL
ESCALA 1 : 100

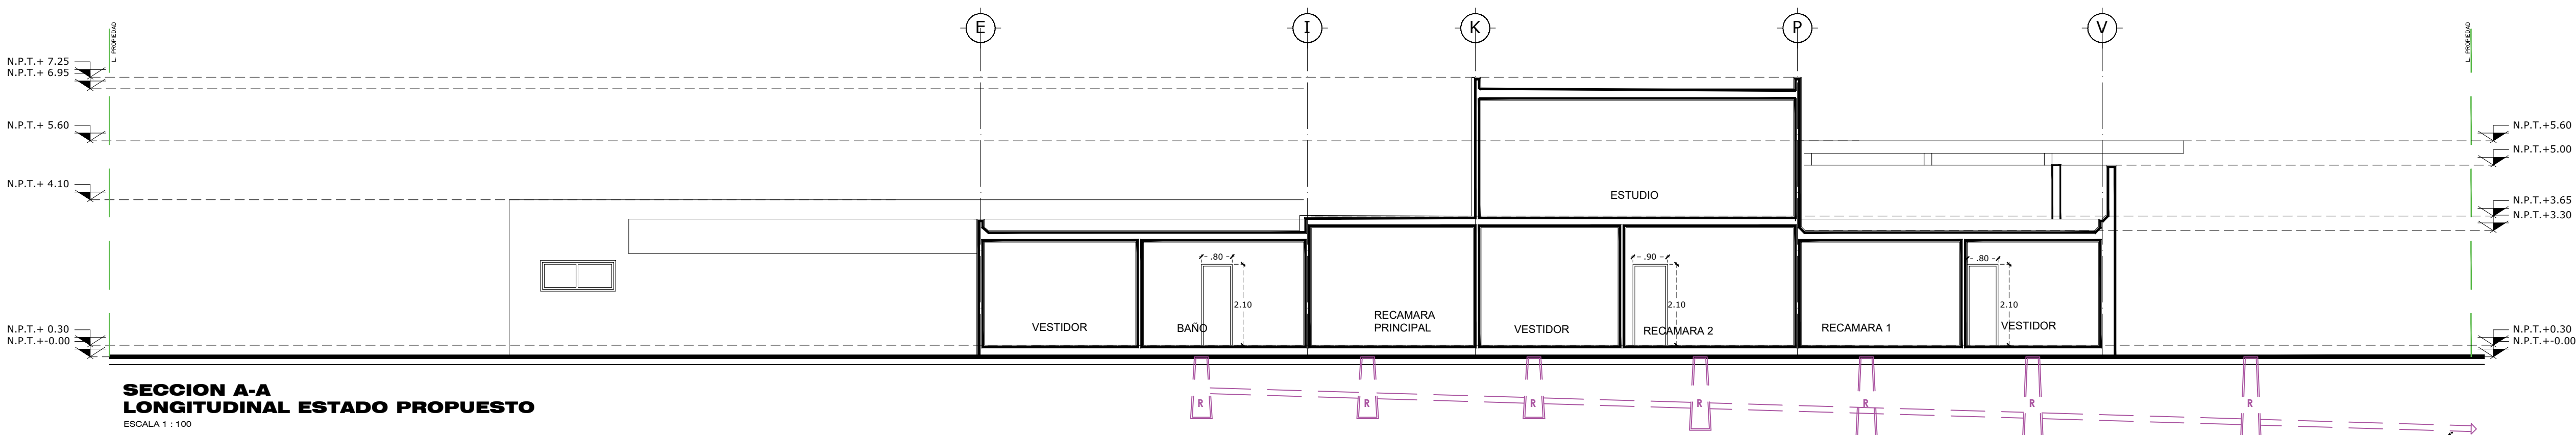


SECCION A-A
LONGITUDINAL ESTADO PROPUESTO
ESCALA 1 : 100

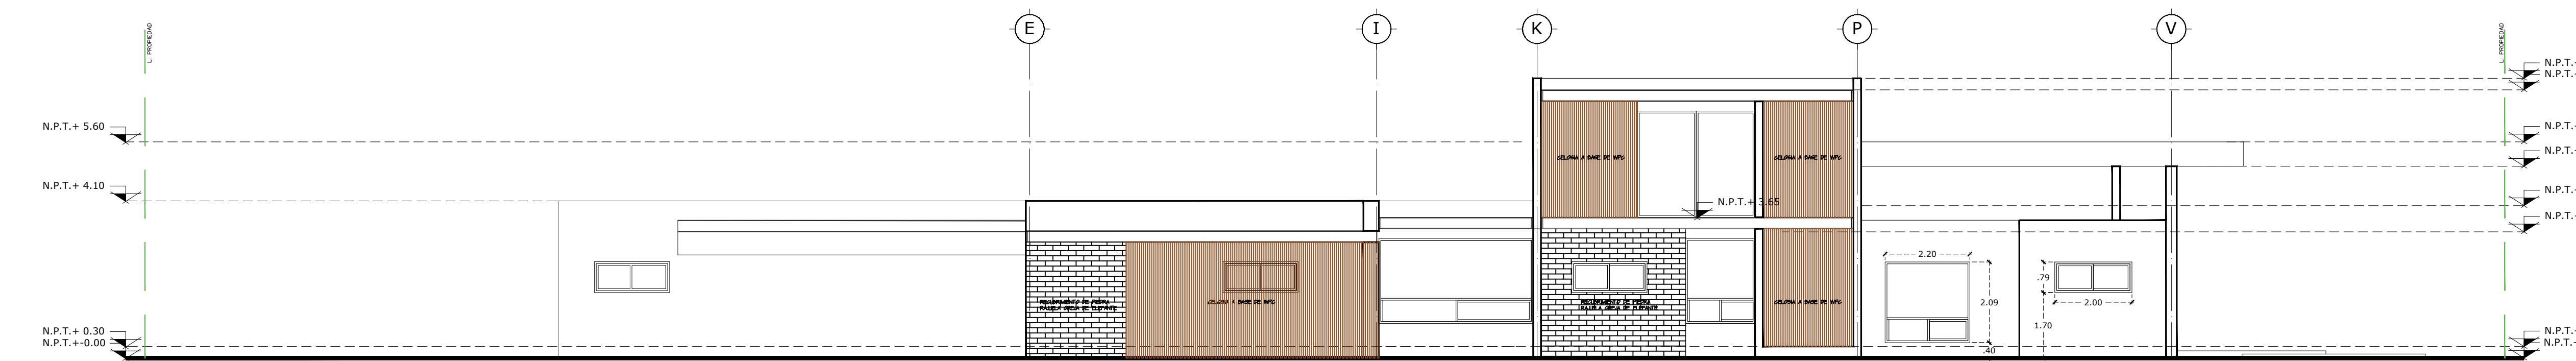


ALZADO ESTADO PROPUESTO
02
ESCALA 1 : 100



UBICACIÓN

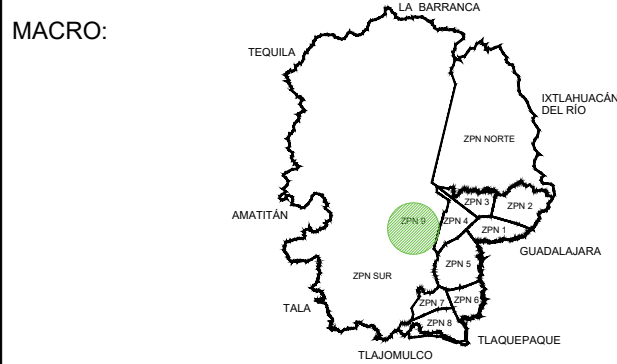

LOCALIZACIÓN MICRO:

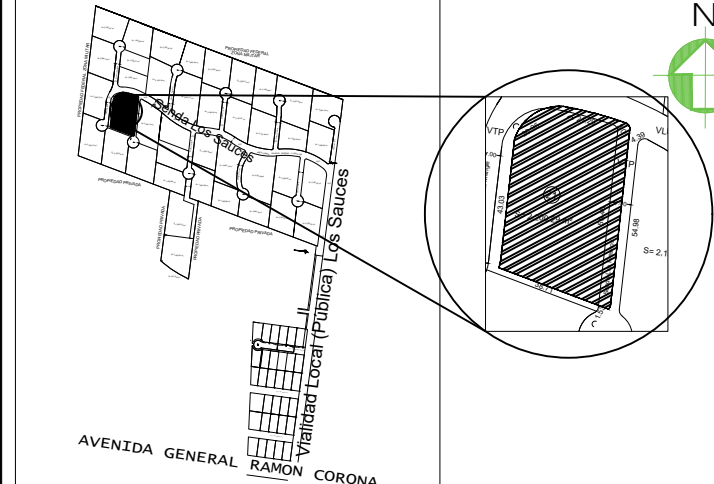

CUADRO DE ÁREAS

	ACTUAL	PROPUESTO
TERRENO	2200.29 m2	2200.29 m2
PLANTA BAJA	595.59 m2	749.83 m2
PLANTA ALTA	--- m2	118.32 m2
TOTAL	595.59 m2	868.15 m2
CUBIERTA LIGERA	15.16 m2	

NOTA: CUALQUIER ELEMENTO CONSTRUCTIVO NO SEÑALADO
DEBERÁ ANOTARSE EN ESTE RECUADRO.

COEFICIENTES

	C.O.S.	C.U.S.
PERMITIDO	0.4 880 m2	0.7 1540 m2
PROYECTADO	0.34 749.8m2	0.4 868.1m2

SIMBOLOGÍA

AMPLIACION	272.46m2
DESMONTAR	23.7m2

DATOS DEL PREDIO

CALLE: LOS SAUCES		
NÚMERO:	CONDominio: RANCHO LOS SAUCES	
LOTE 21	MANZANA	UP
COLONIA:FRACC. LOS SAUCES		
PROPIETARIO(S)		
GUILLERMO OROZCO VALENZUELA		

FIRMA

DIRECTOR RESPONSABLE EN PROYECTO Y OBRA
RICARDO ORTIZ FLORES
DRZ- 0424/2026

FIRMA


DIBUJO: SYD CONSTRUCTORES

TÍTULO
AMPLIACION SAUCES

CONTENIDO


ALZADOS

ESCALA	FECHA	NÚMERO DE
1:100	ABRIL 2026	LÁMINA
		7/7

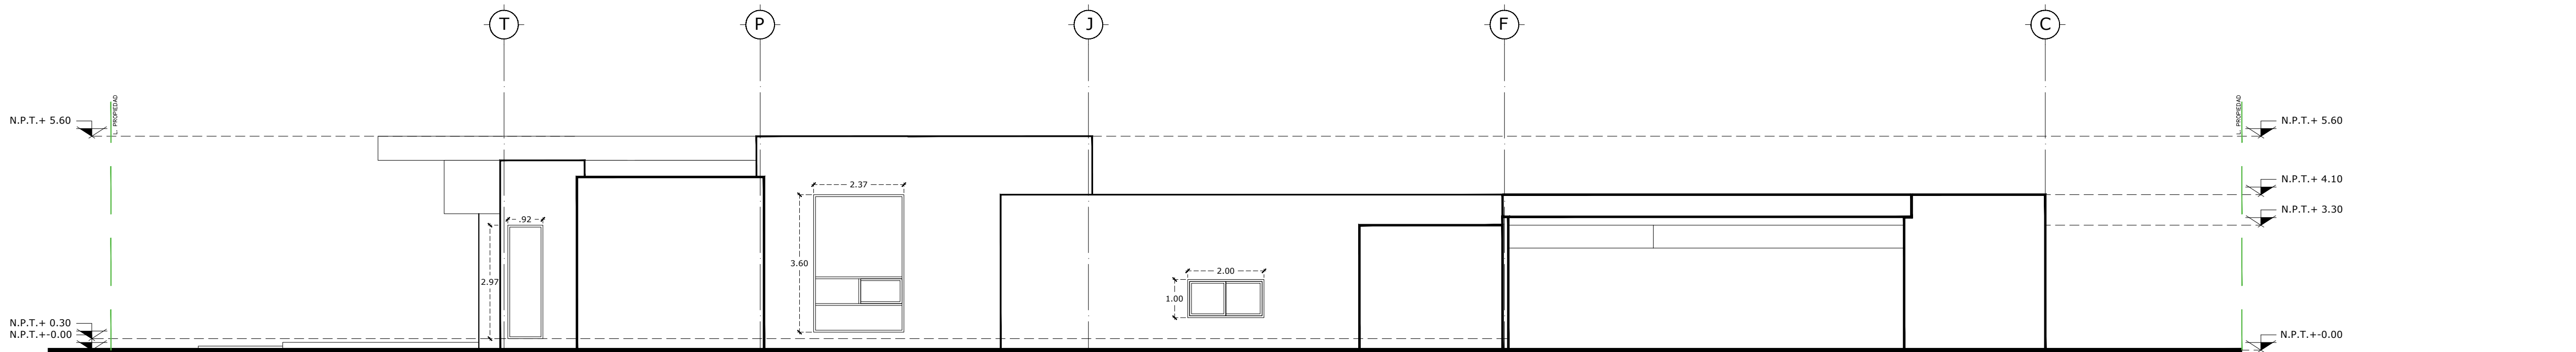


ALZADO ESTADO ACTUAL
04

ESCALA 1 : 100

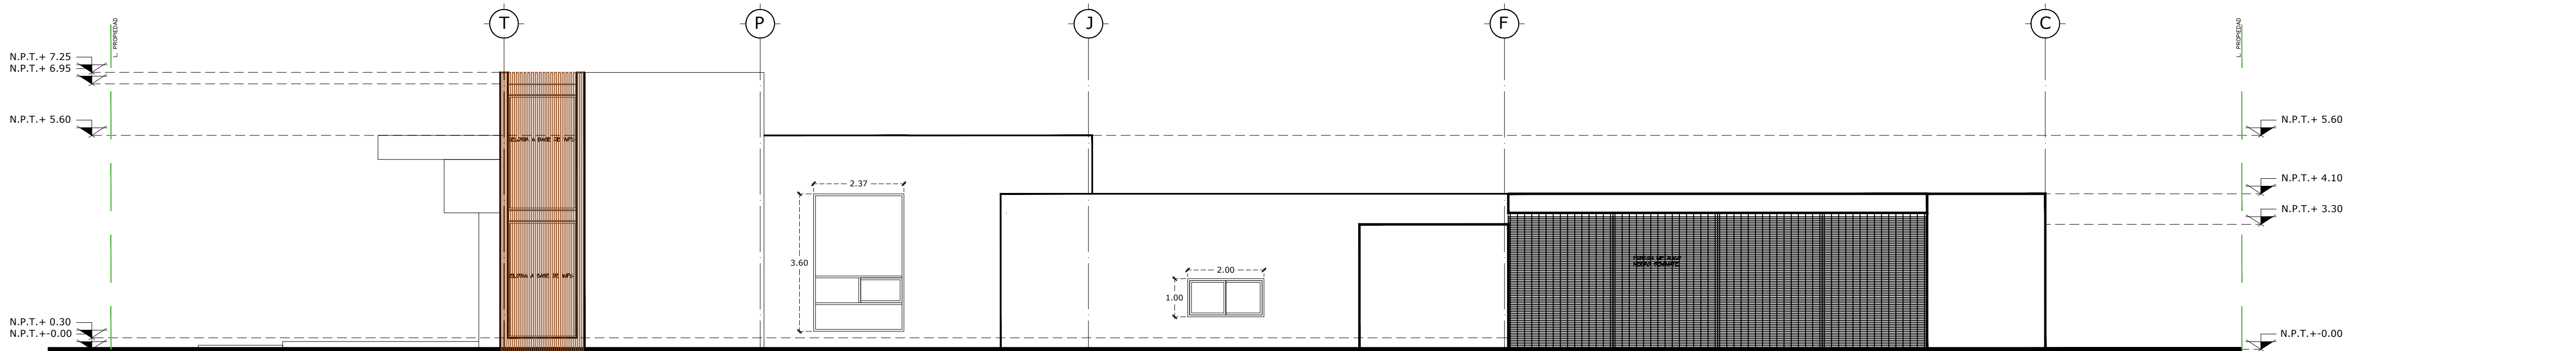


ALZADO ESTADO PROPUESTO
04

ESCALA 1 : 100

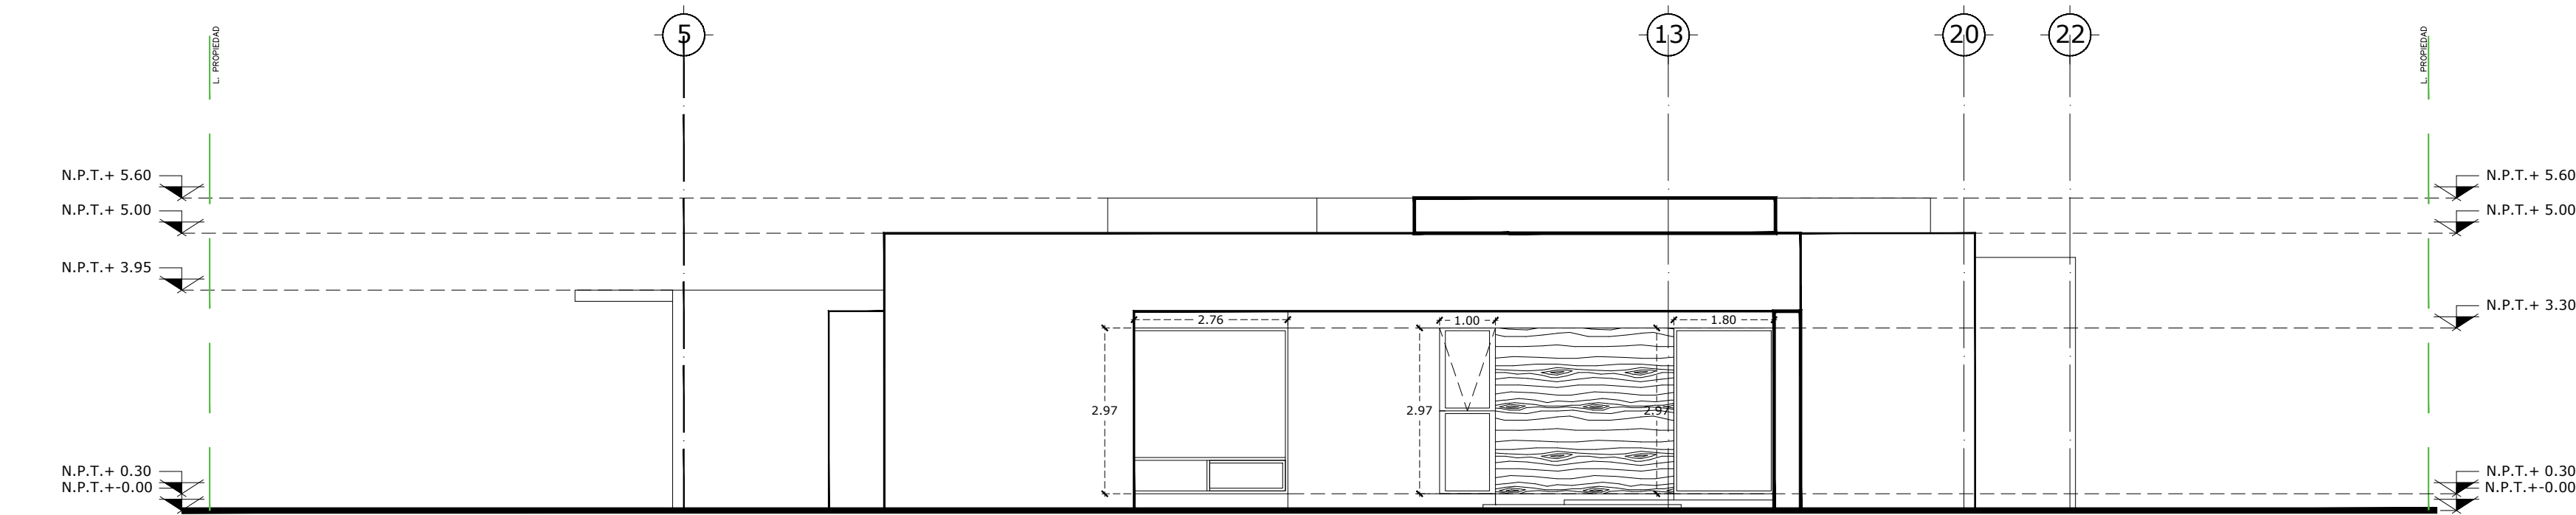


ALZADO ESTADO ACTUAL
03

ESCALA 1 : 100

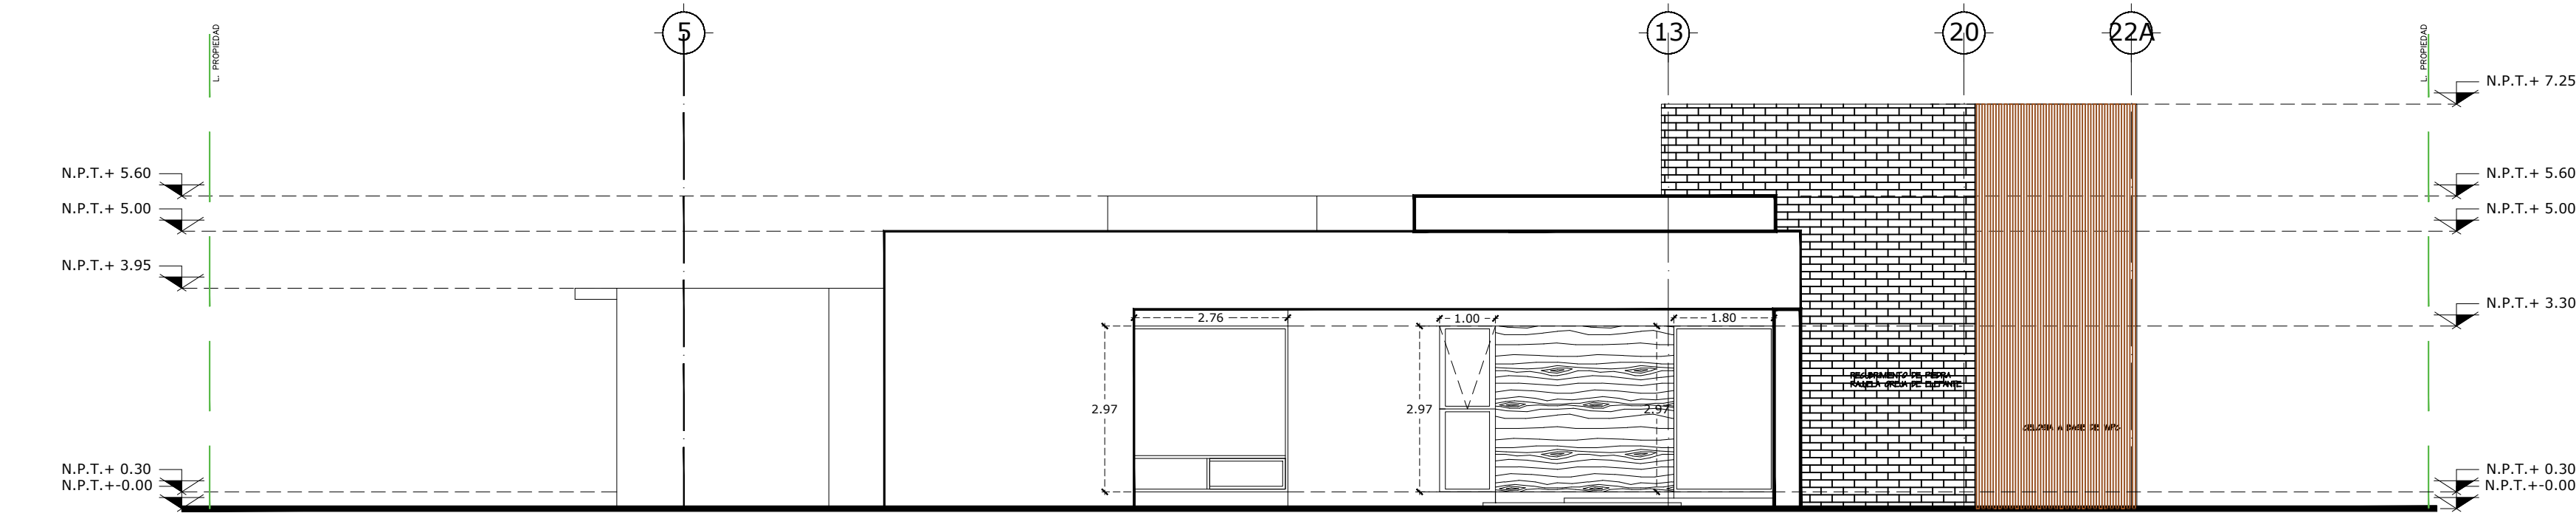

ALZADO ESTADO PROPUESTO
03

ESCALA 1 : 100

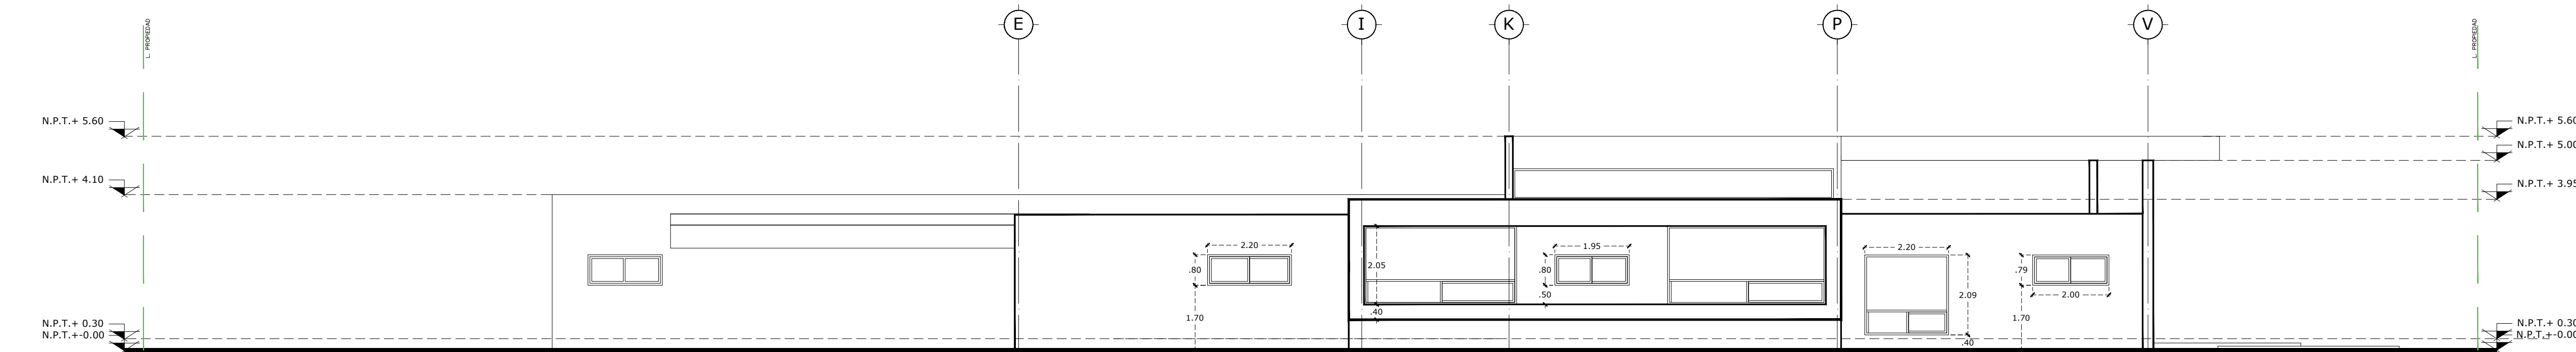

ALZADO ESTADO ACTUAL
02

ESCALA 1 : 100



PLANTA BAJA JARDINERIA
ESCALA 1:100

SIMBOLOGIA INST. ELECTRICA

- TABLERO GENERAL
- MEDIDOR
- REGISTRO
- BOMBA 1/2 HP
8 Mcprada. Centrifuga de succión frontal de un paso. 500W
- SALIDA DE CENTRO
(Segun detalle)
- ARBOTANTE
(Segun detalle)
- MULTICONTACTO EN MURO
Biceno Malt. Color negro
Doble. 2 x 125W
- CONTACTO EN MURO
Biceno Malt. Color negro
Sencillo. 125W
- APAGADOR
Biceno Malt. Color verde. A-Doble
- SUBE TUBERIA
Pulido de 25mm.
- LINEA POR MURO
Pulido de 19 mm.
- LINEA POR LOSA

SIMBOLOGIA

- TUERCA UNION
- MEDIDOR
- VALVULA DE COMPUERTA O DE GLOBO
- Llave de NARIZ
- VALVULA CHECK
- TUBERIA DE AGUA FRIA EN DIAMETRO INDICADO
- TUBERIA DE AGUA CALIENTE EN DIAMETRO INDICADO
- BAF
SUBE AGUA FRIA
- BAF
SUBE AGUA CALIENTE
- BAF
BAJA AGUA FRIA
- BAF
BAJA AGUA CALIENTE
- REGISTRO SANITARIO DE 40x60 cm con COLADERA
- TUBERIA SANITARIA DE PVC DE DIAMETRO INDICADO
- ALBANAL DE CONCRETO SIMPLE 15cm (6") DIAM
- BAF
BAJADA DE AGUA PLUVIAL
- NIVEL DE PISO TERMINADO
- NIVEL DE PLANTILLA

N O T A : La tubería que se empleara en la instalación hidráulica será de cobre

ESPECIFICACIONES GENERALES PARA LA INSTALACION HIDRAULICA

- DEBERA UTILIZARSE TUBERIA DE COBRE TIPO "M" CUANDO ESTA QUEDE AHOGADA EN MUROS O LOSAS DEL DIAMETRO ESPECIFICADO.
- DEBERA UTILIZARSE TUBERIA DE FIERRO GALVANIZADO CEDULA 40 EN LOS LUGARES DONDE LA TUBERIA SE ENCUENTRE EXPUESTA AL MEDIO AMBIENTE.
- PROBAR LA TUBERIA DE AGUA A PRESION DE 5 Kg/cm2 DURANTE 2 HORAS MINIMO.
- LA ALIMENTACION DE TOMA DOMICILIARIA A LA RED INTERIOR SERA DE TUBERIA GALVANIZADA DE 19MM
- NO CUBRIR NINGUNA INSTALACION HASTA DESPUES DE DIAMETRO DE SER PROBADA.
- DIAMETRO DE TUBERIA INDICADA EN PULGADAS.

AREA A CONSTRUIR

ITEM	2000.29	M2	2000.29	M2
PLANTA BAJA	600.35	M2	141.39	M2
TOTAL	600.35	M2	141.39	M2

PROYECTO:
CASA HABITACIÓN

PROPIETARIO:
Guillermo Orozco Valenzuela

UBICACIÓN:
Fraccionamiento Los Sauces, c/ Senda de los Sauces, Zapopan, Jalisco

PERITO RESPONSABLE:
CED. PROFESIONAL: CLAVE MUNICIPAL:

PROYECTO:
SYD CONSTRUCTORES

PLANO:
PLANTA BAJA JARDINERIA

LAMINA:
UNICA

ESCALA:
INDICADA

COTAS:
METROS

FECHA:
NOVIEMBRE 2025